
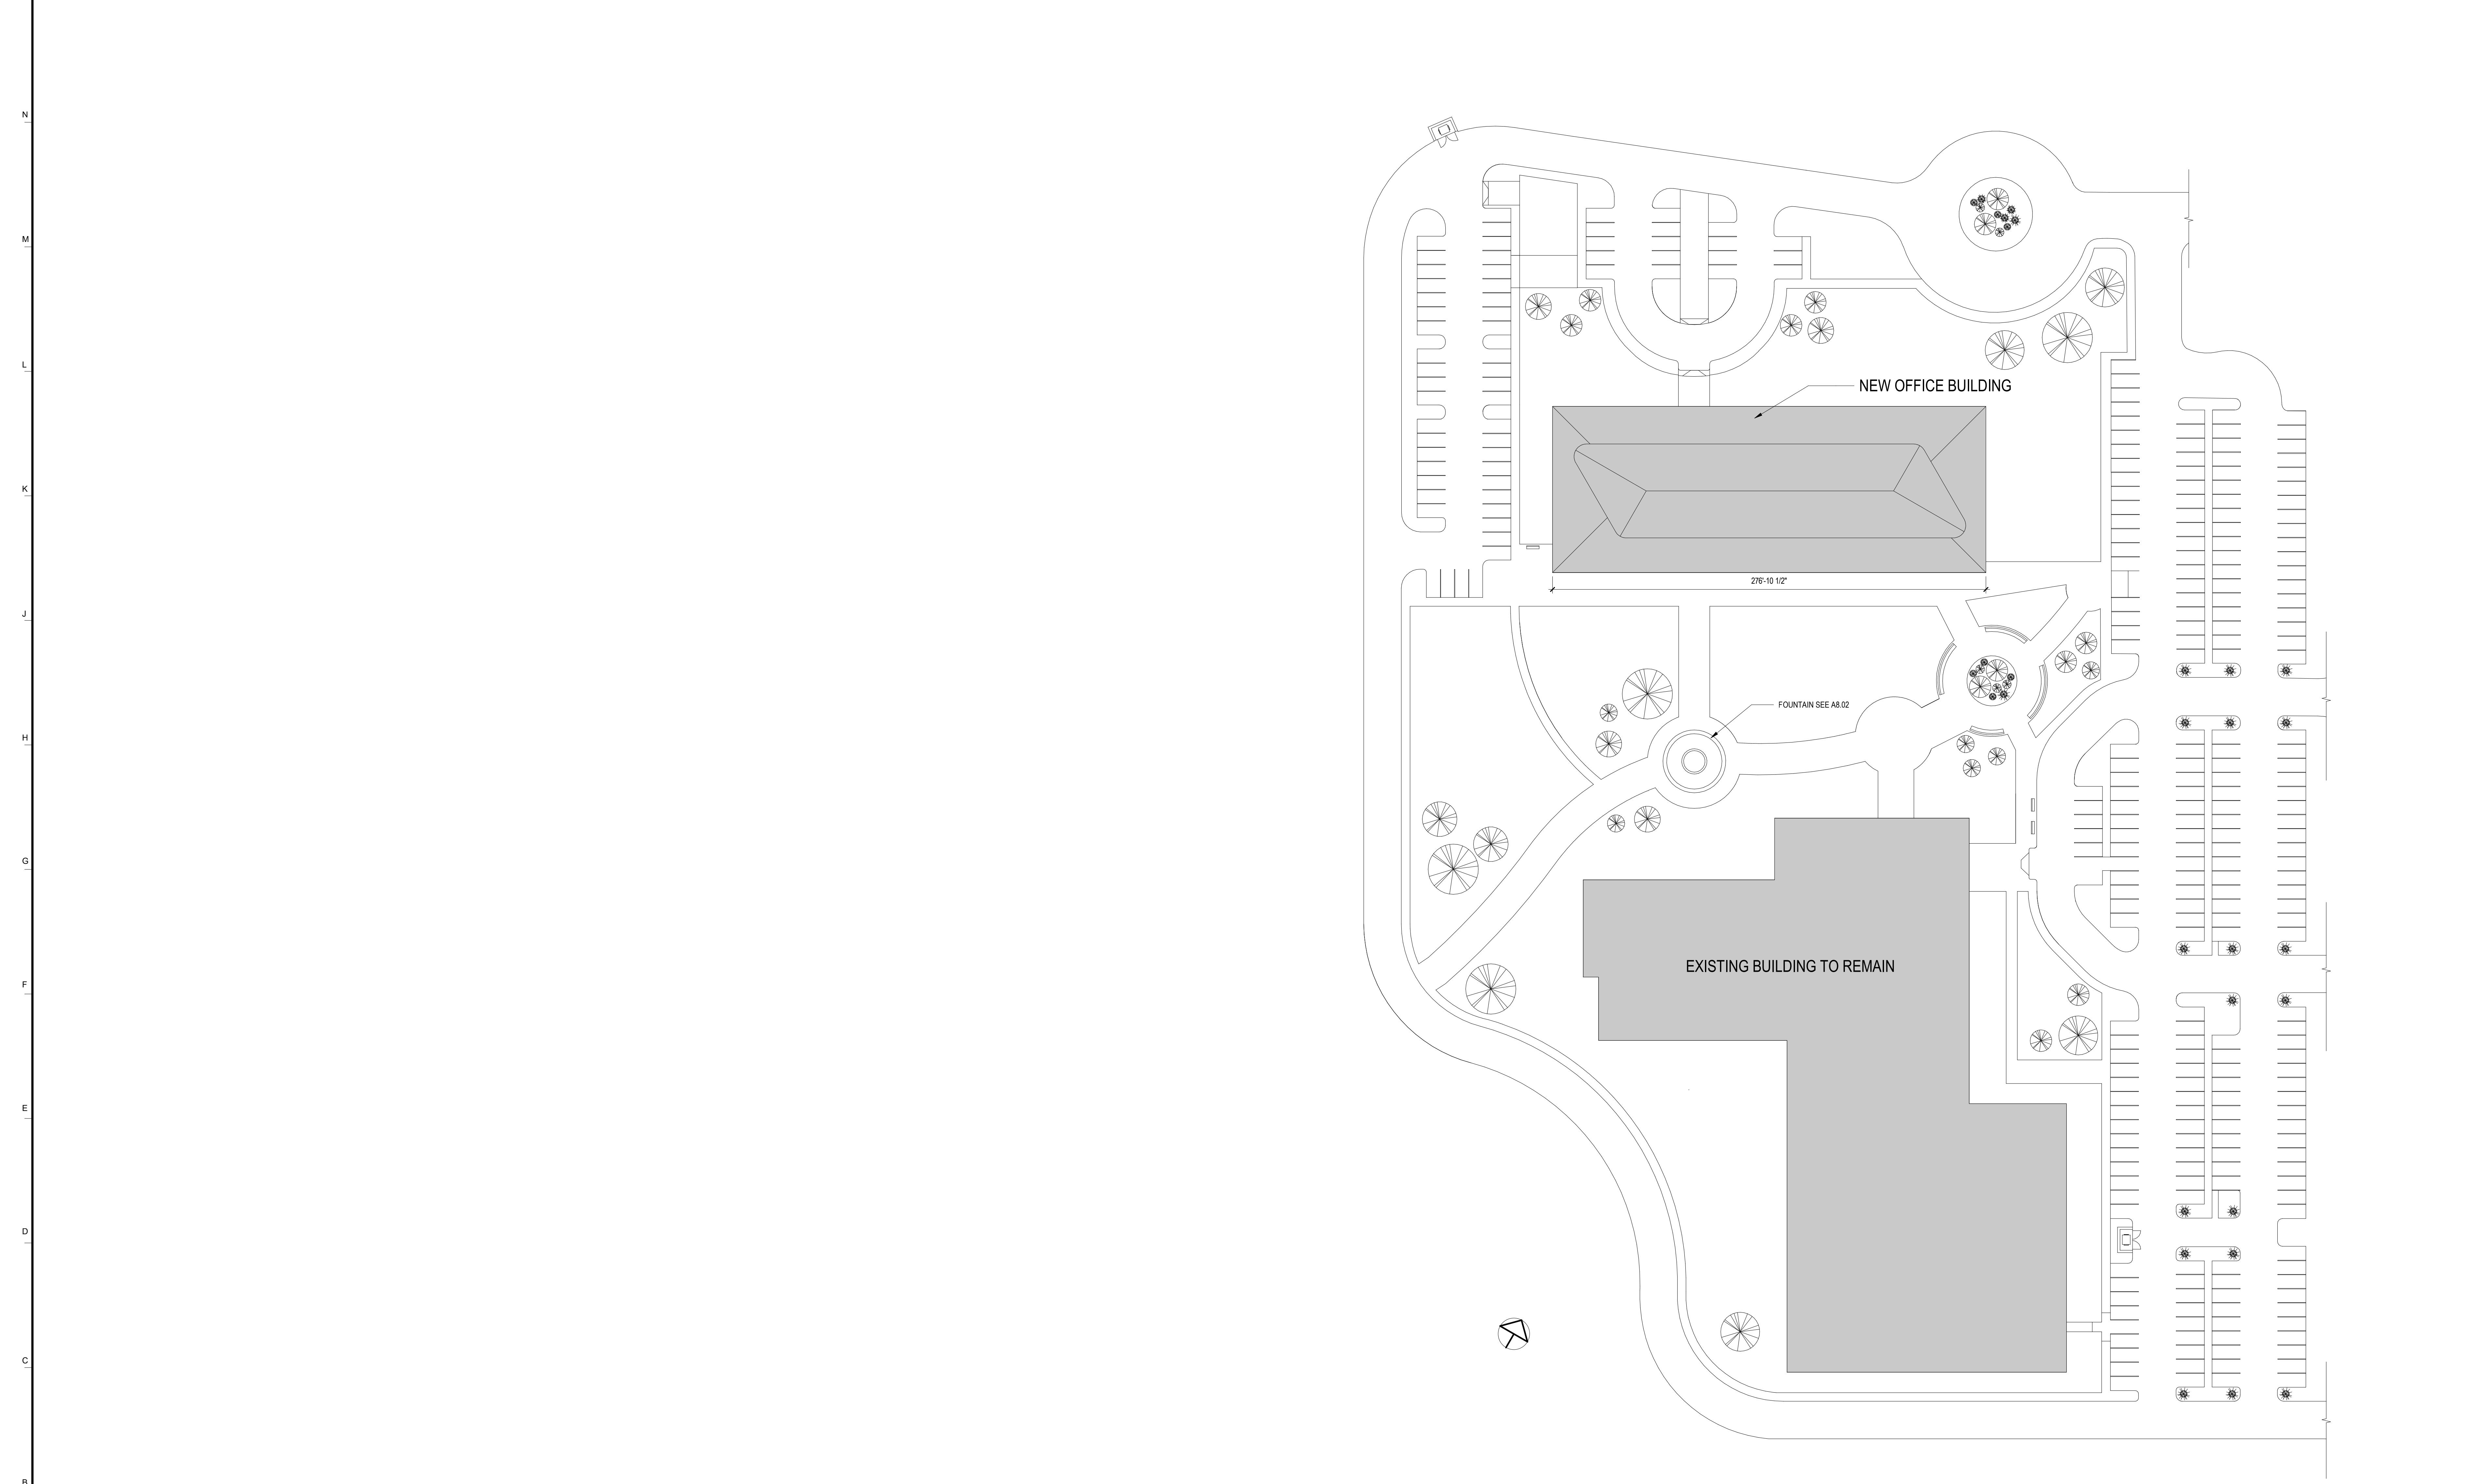




15 | 14 | 13 | 12 | 11 | 10 | 9 | 8 | 7 | 6 | 5 | 4 | 3 | 2 | 1 |

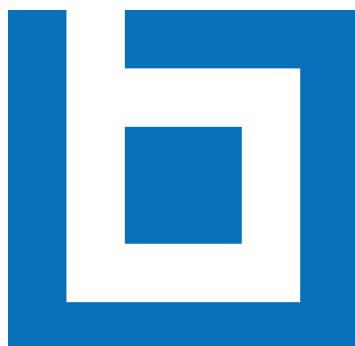

Site Plan 1
SCALE: 1" = 40'-0"

 BLUEBEAM® A NEMETSCHEK COMPANY	CAPTURE ENGINEERS Mechanical Electrical Plumbing 1234 Miller St. Manchester, NH 06930	REVU ARCHITECTS 5555 N. Broad St Pasadena CA 91101	OFFICE BUILDING Project No: 323232 Project Address: 123 Schonsett St Chicago, IL 60601	THIS DRAWING IS INTENDED FOR DEMONSTRATION PURPOSES ONLY. DO NOT USE THIS DRAWING FOR ANY OTHER PURPOSE WITHOUT THE EXPRESS WRITTEN PERMISSION OF BLUEBEAM, INC.	DATE ISSUED FOR: 03/04/2019 INTERNAL REVIEW PROJECT: 3232 DRAWN BY: Author CHECKED BY: Checker APPROVED BY: Approver # DATE DESCRIPTION	NOT FOR CONSTRUCTION CONFIDENTIAL	STAMP:	STAMP:	SHEET TITLE & NUMBER SITE PLAN A1.01
--	--	--	--	--	--	--	--------	--------	--

15 | 14 | 13 | 12 | 11 | 10 | 9 | 8 | 7 | 6 | 5 | 4 | 3 | 2 | 1 |

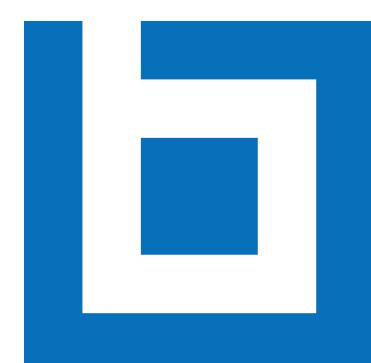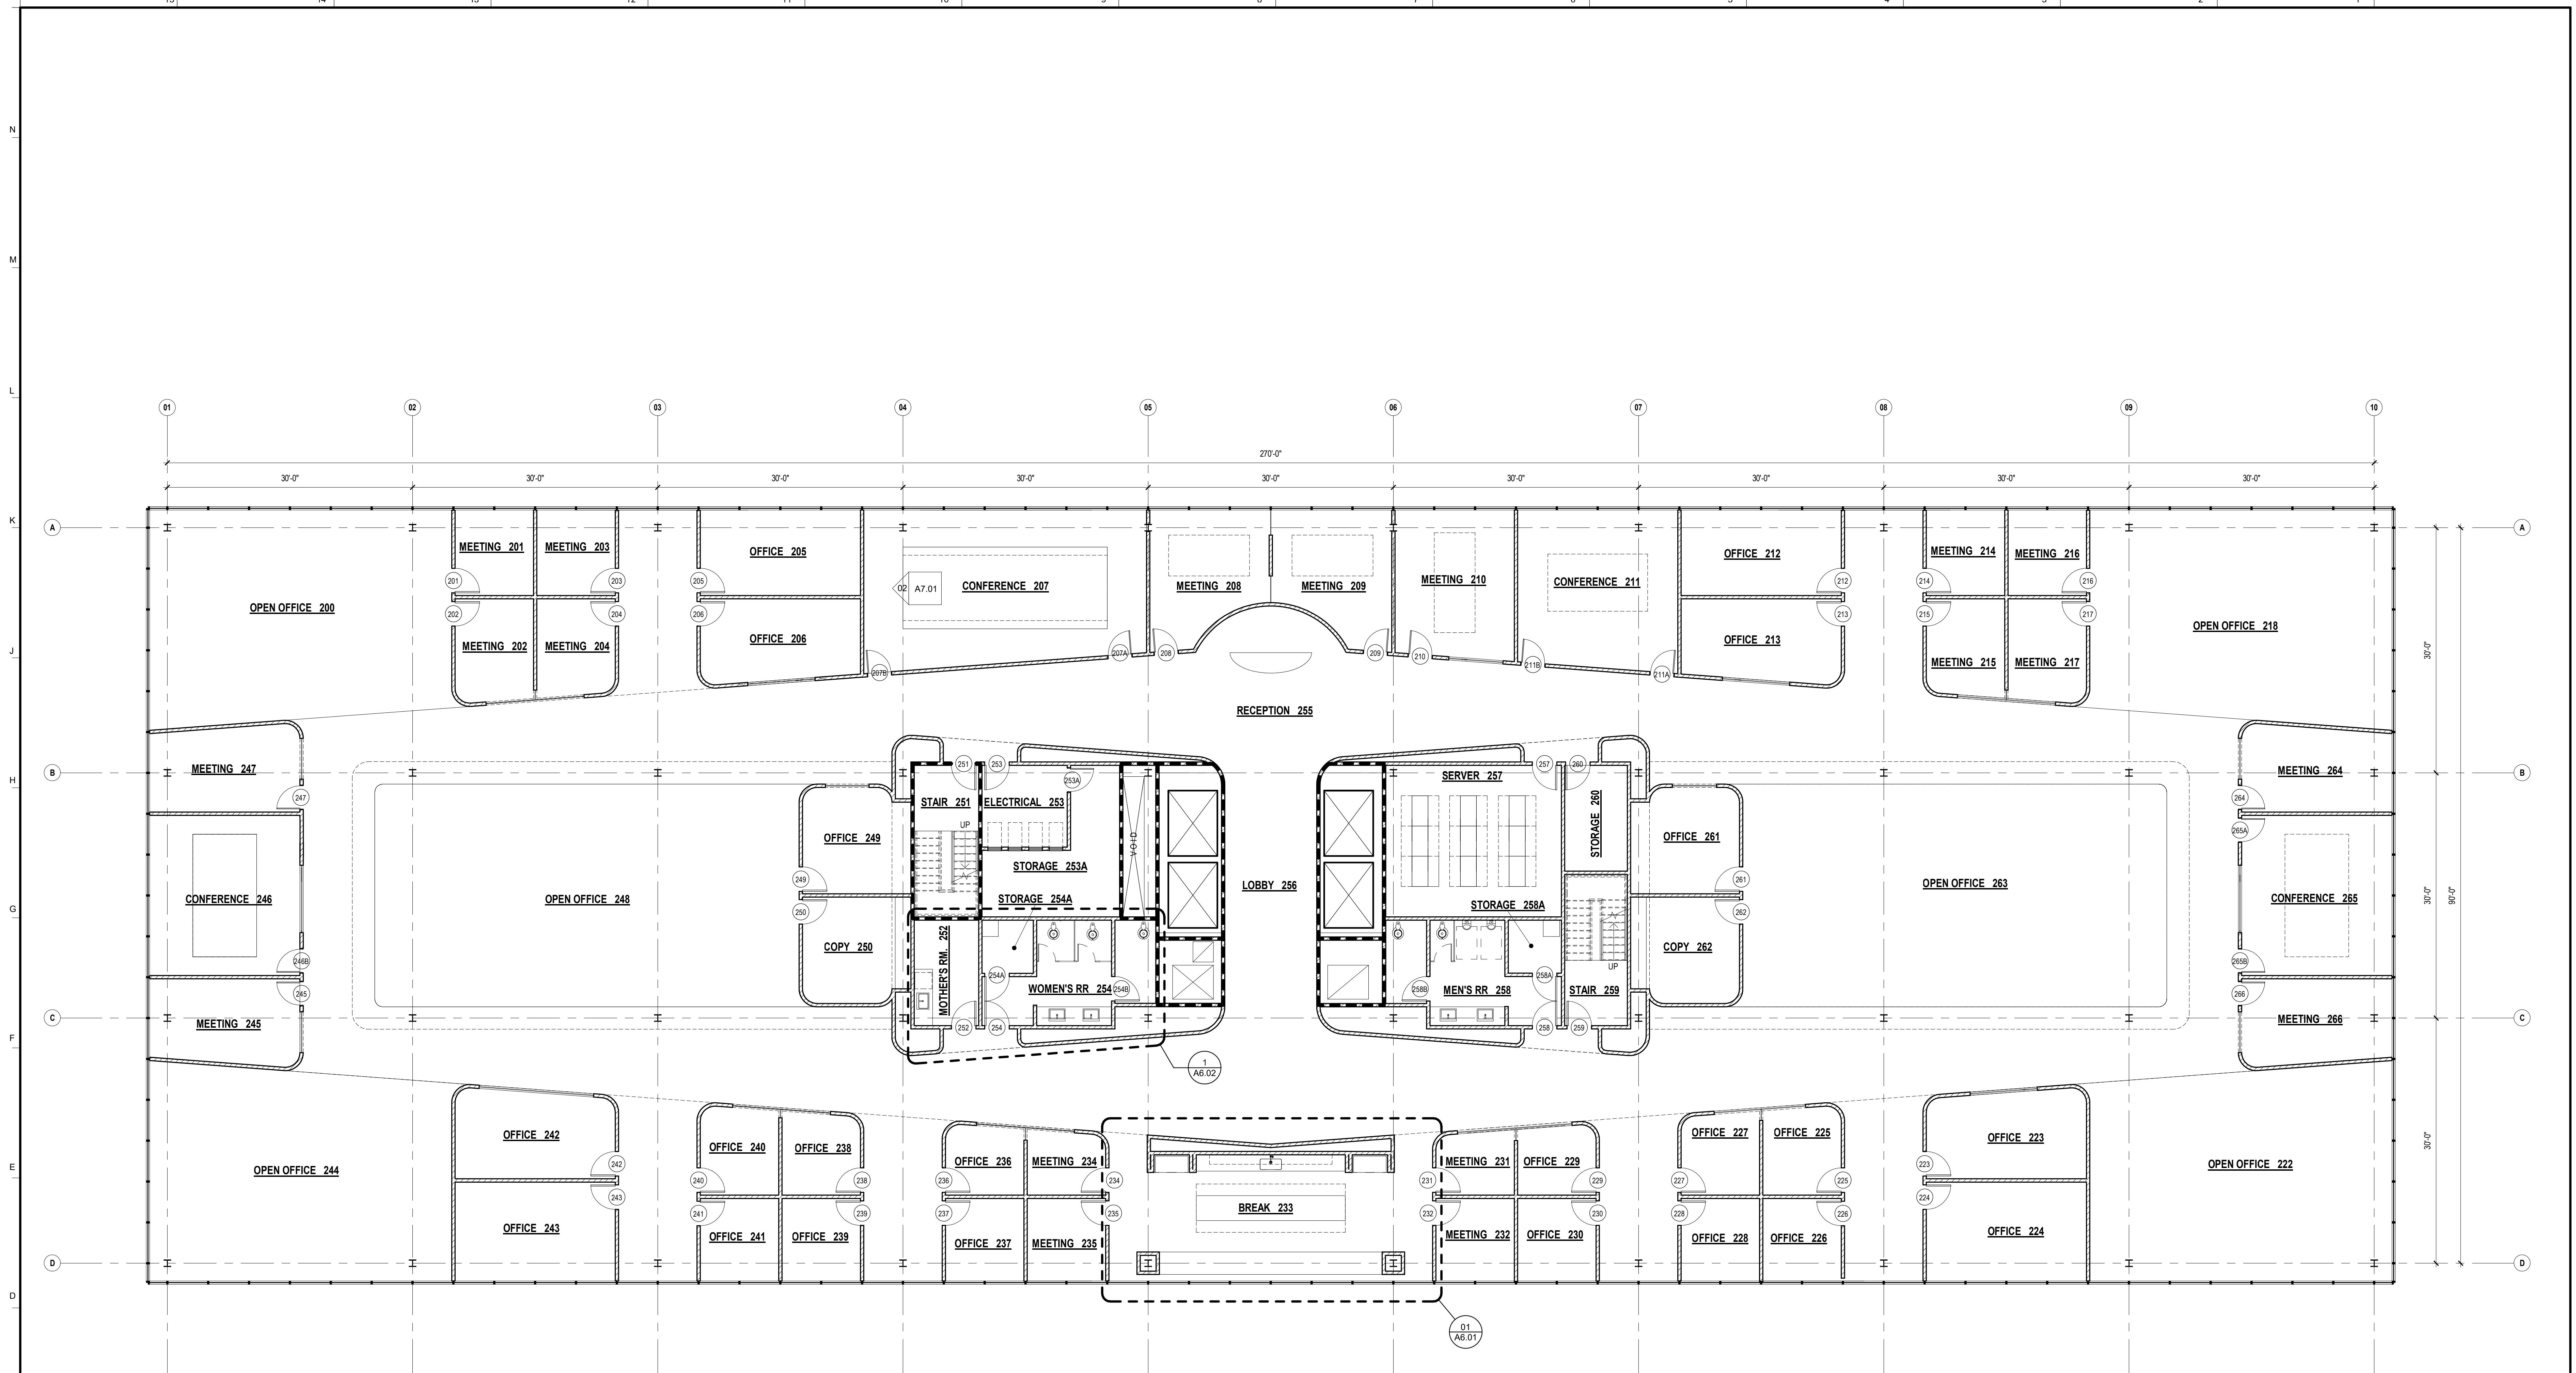

BLUEBEAM®
A NEMETSCHEK COMPANY

CAPTURE ENGINEERS
Mechanical
Electrical
Plumbing

1234 Miller St.
Manchester, NH 06930

REVU ARCHITECTS
Project No: 323232
5555 N. Broad St
Pasadena CA 91101

OFFICE BUILDING
Project Address:
123 Schonsett St
Chicago, IL 60601

THIS DRAWING IS INTENDED FOR
DEMONSTRATION PURPOSES
ONLY. DO NOT USE THIS
DRAWING FOR ANY OTHER
PURPOSE WITHOUT THE
EXPRESS WRITTEN PERMISSION
OF BLUEBEAM, INC.

DATE ISSUED FOR: 03/04/2019
INTERNAL REVIEW
PROJECT: 3232
DRAWN BY: Author
CHECKED BY: Checker
APPROVED BY: Approver
DATE: DESCRIPTION

**NOT FOR
CONSTRUCTION**
CONFIDENTIAL

STAMP:


STAMP:

SHEET TITLE & NUMBER
LEVEL 02 FLOOR PLAN

A2.2.1

© 2018 Bluebeam, Inc.

15 | 14 | 13 | 12 | 11 | 10 | 9 | 8 | 7 | 6 | 5 | 4 | 3 | 2 | 1 |

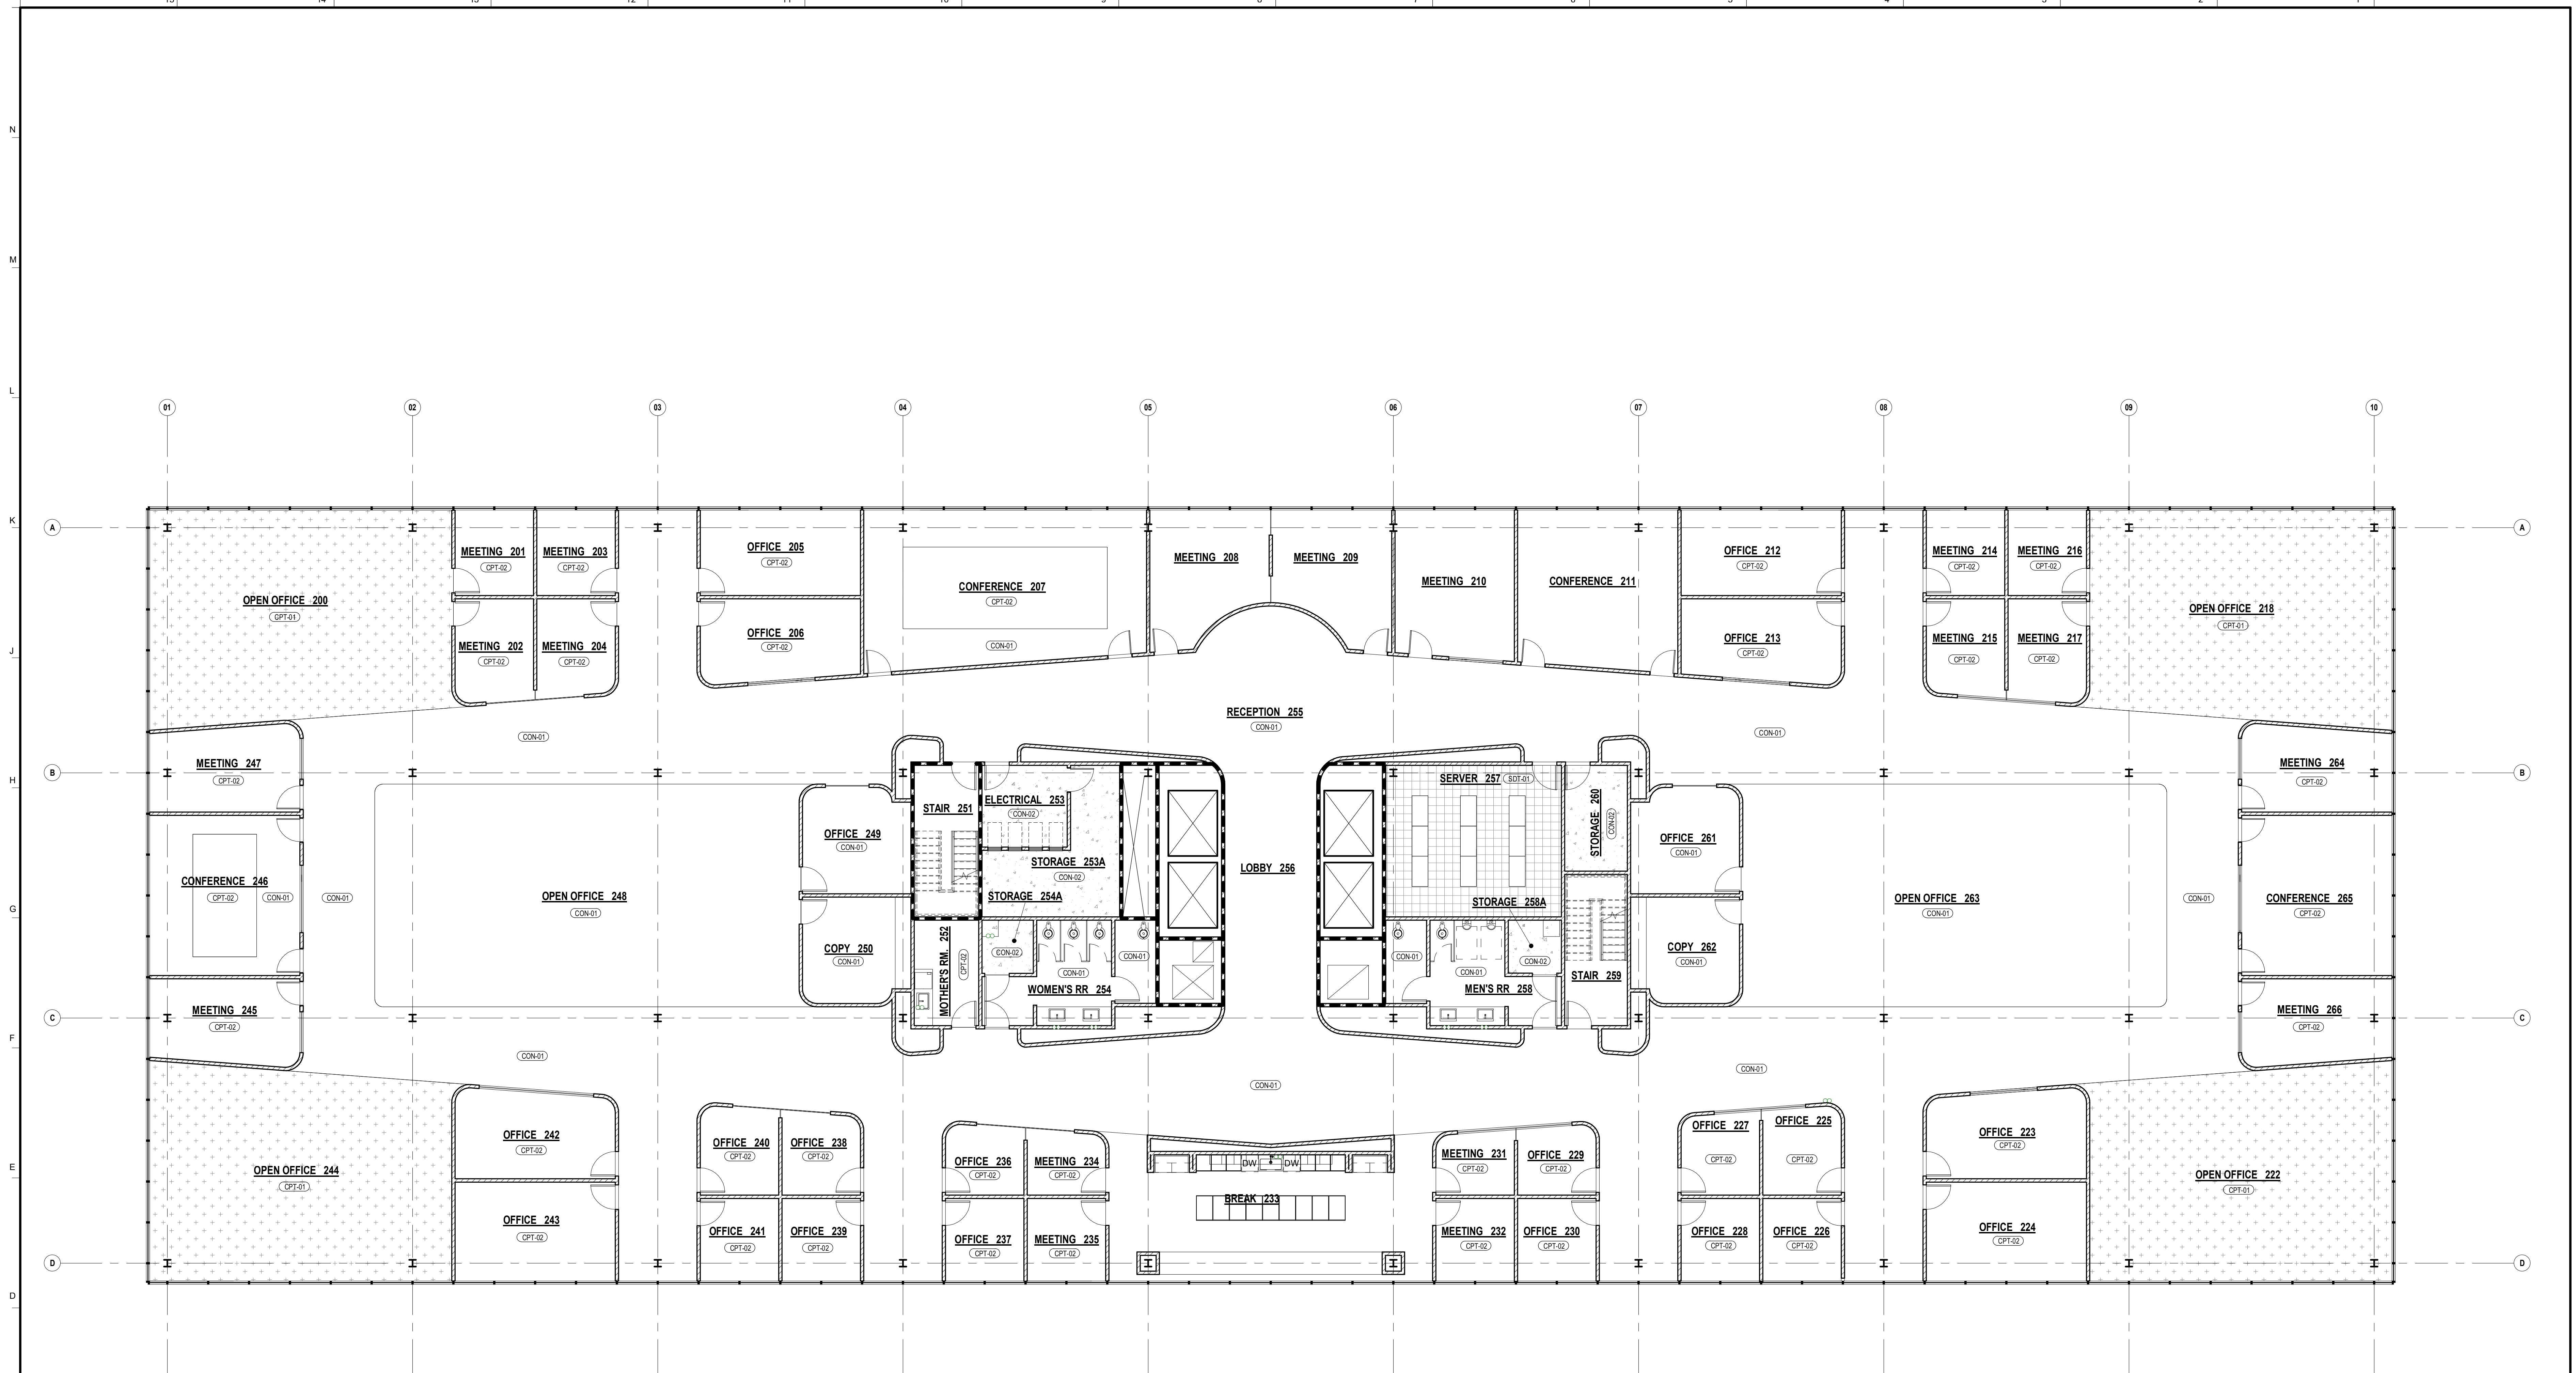

BLUEBEAM®
A NEMETSCHEK COMPANY

CAPTURE ENGINEERS
Mechanical
Electrical
Plumbing

1234 Miller St.
Manchester, NH 06930

REVU ARCHITECTS
Project No: 323232
5555 N. Broad St
Pasadena CA 91101

OFFICE BUILDING
Project Address:
123 Schonsett St
Chicago, IL 60601

THIS DRAWING IS INTENDED FOR
DEMONSTRATION PURPOSES
ONLY. DO NOT USE THIS
DRAWING FOR ANY OTHER
PURPOSE WITHOUT THE
EXPRESS WRITTEN PERMISSION
OF BLUEBEAM, INC.

DATE ISSUED FOR: 03/04/2019
INTERNAL REVIEW
PROJECT: 3232
DRAWN BY: Author
CHECKED BY: Checker
APPROVED BY: Approver
DATE DESCRIPTION

**NOT FOR
CONSTRUCTION**
CONFIDENTIAL


STAMP:

STAMP:

SHEET TITLE & NUMBER
LEVEL 02 FINISH
FLOOR PLAN

A2.2.2

© 2018 Bluebeam, Inc.

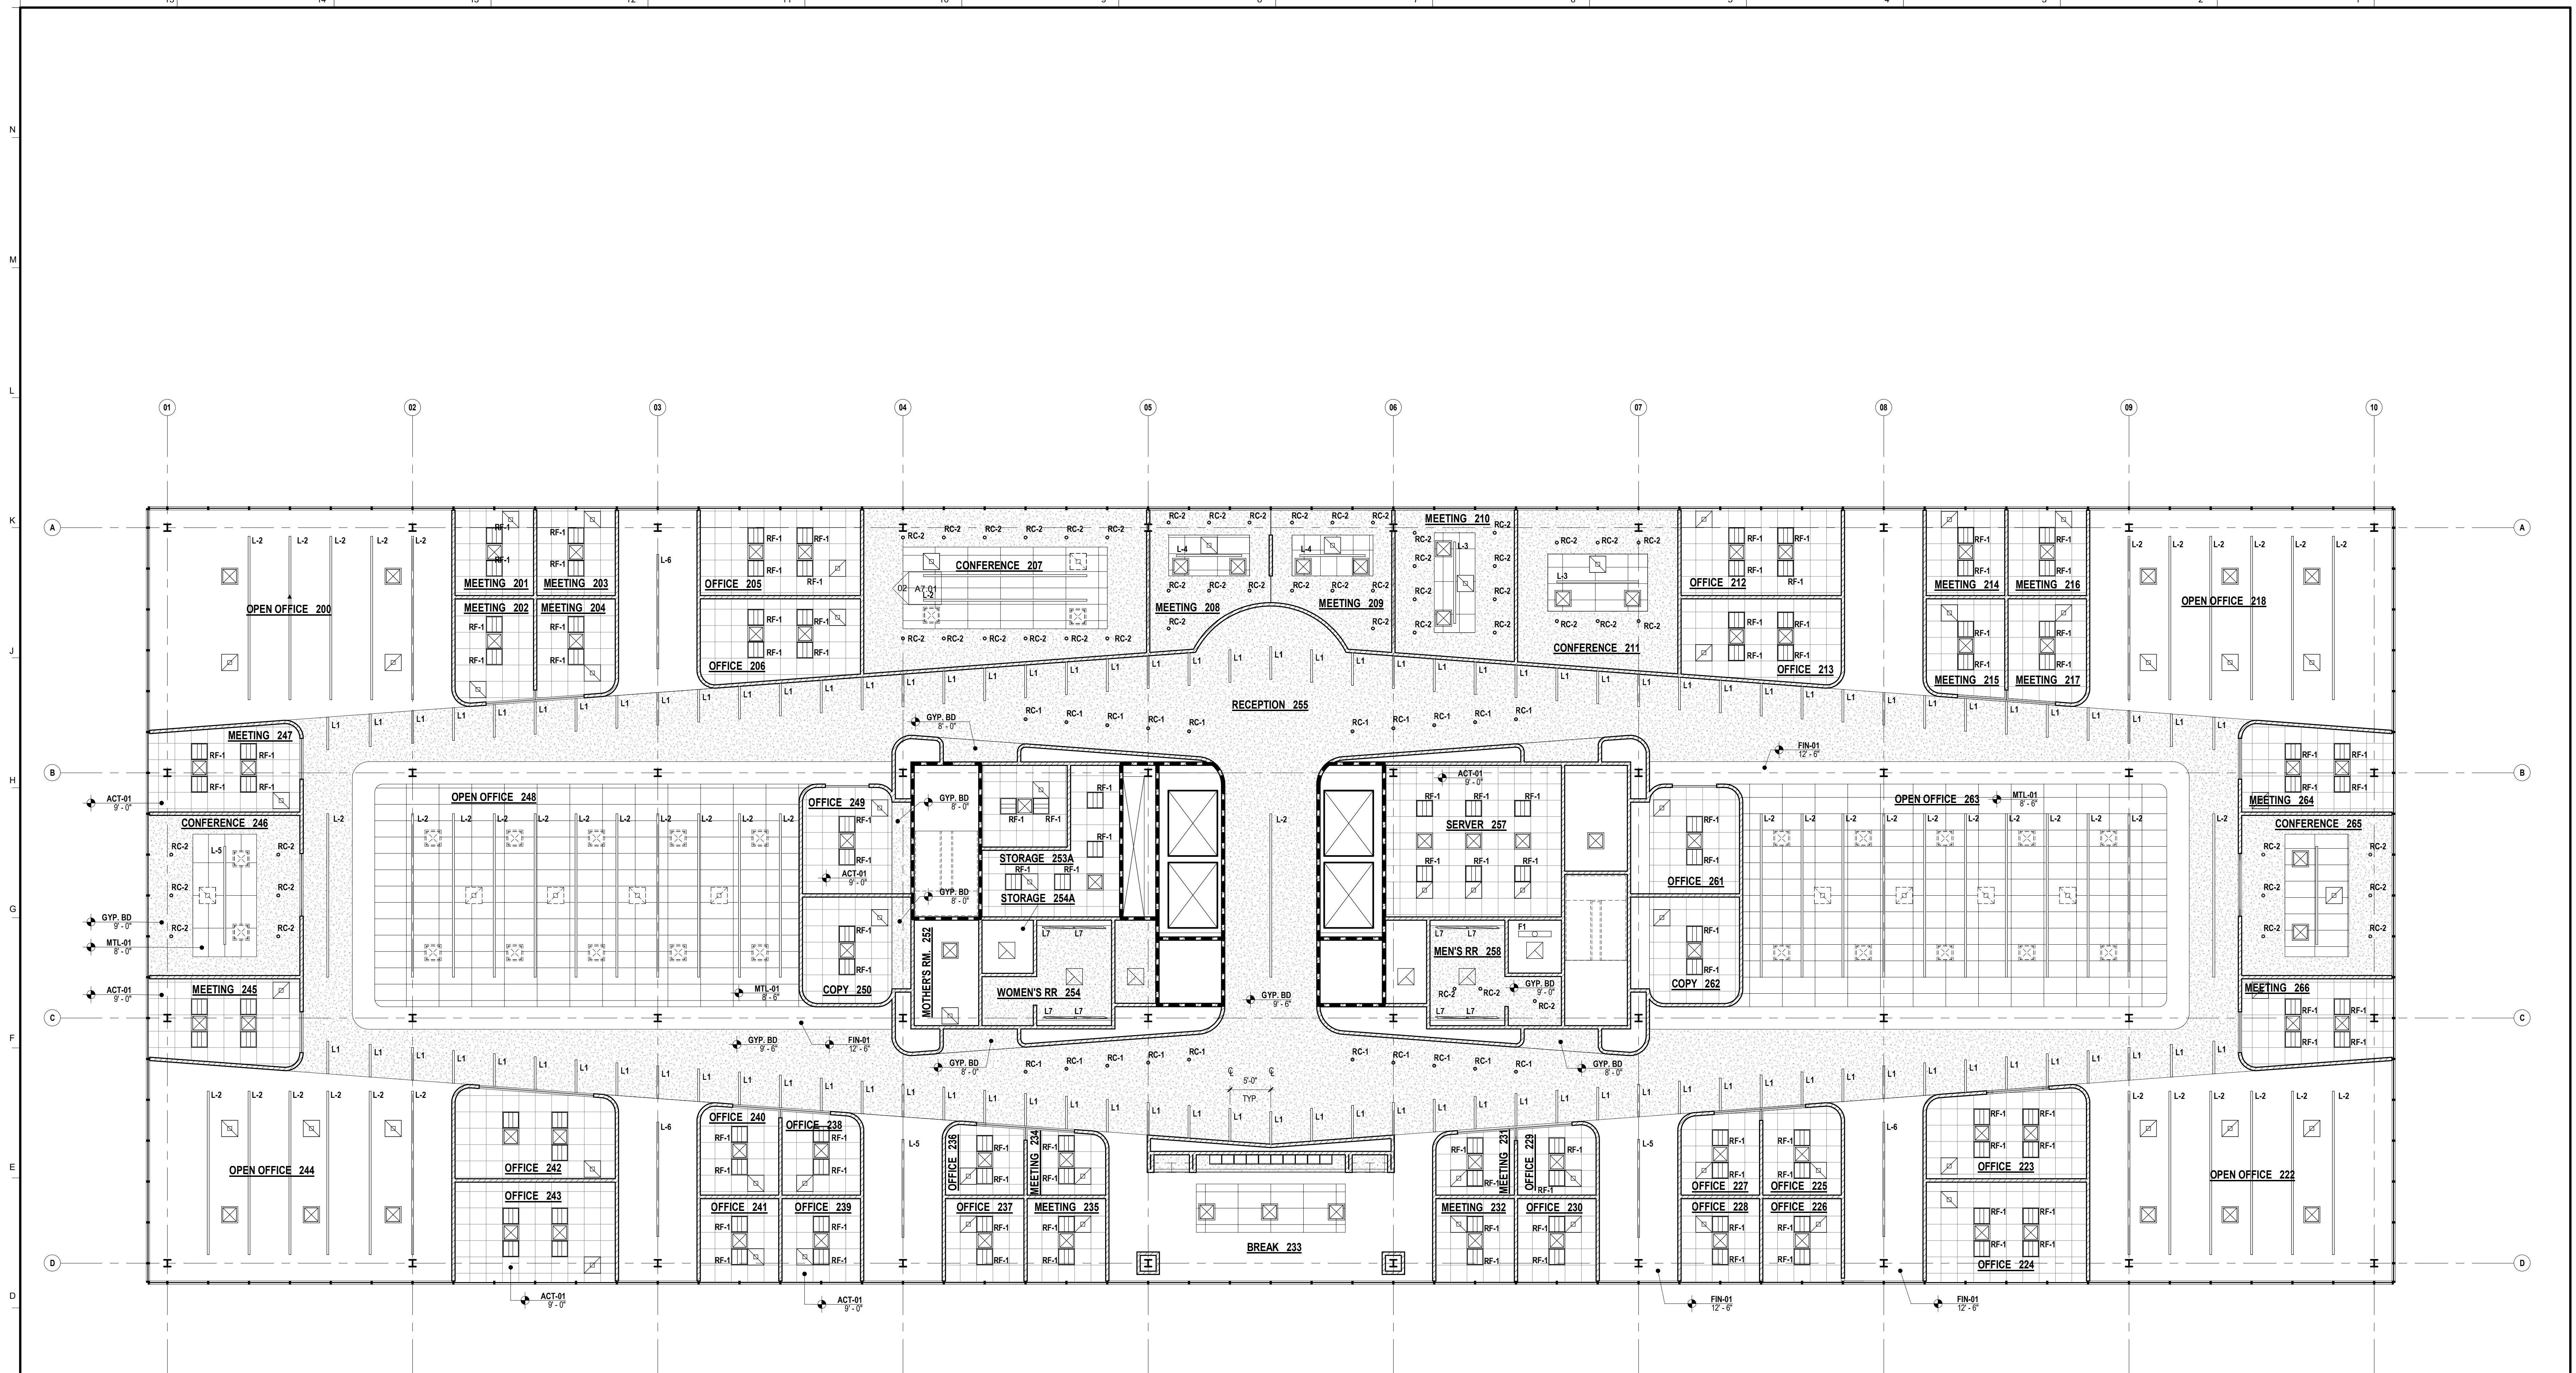

BLUEBEAM®
A NEMETSCHEK COMPANY

CAPTURE ENGINEERS
Mechanical
Electrical
Plumbing

1234 Miller St.
Manchester, NH 06930

REVU ARCHITECTS

5555 N. Broad St
Pasadena CA 91101

OFFICE BUILDING

Project No: 323232

Project Address:
123 Schonsett St
Chicago, IL 60601

THIS DRAWING IS INTENDED FOR
DEMONSTRATION PURPOSES
ONLY. DO NOT USE THIS
DRAWING FOR ANY OTHER
PURPOSE WITHOUT THE
EXPRESS WRITTEN PERMISSION
OF BLUEBEAM, INC.

DATE
03/04/2019
ISSUED FOR: INTERNAL REVIEW
PROJECT
3232
DRAWN BY:
Author
CHECKED BY:
Checker
APPROVED BY:
Approver
| DATE | DESCRIPTION


**NOT FOR
CONSTRUCTION**
CONFIDENTIAL

STAMP:

© 2018 Bluebeam, Inc.

SHEET TITLE & NUMBER
LEVEL 02 REFLECTED
CEILING PLAN

A2.2.3

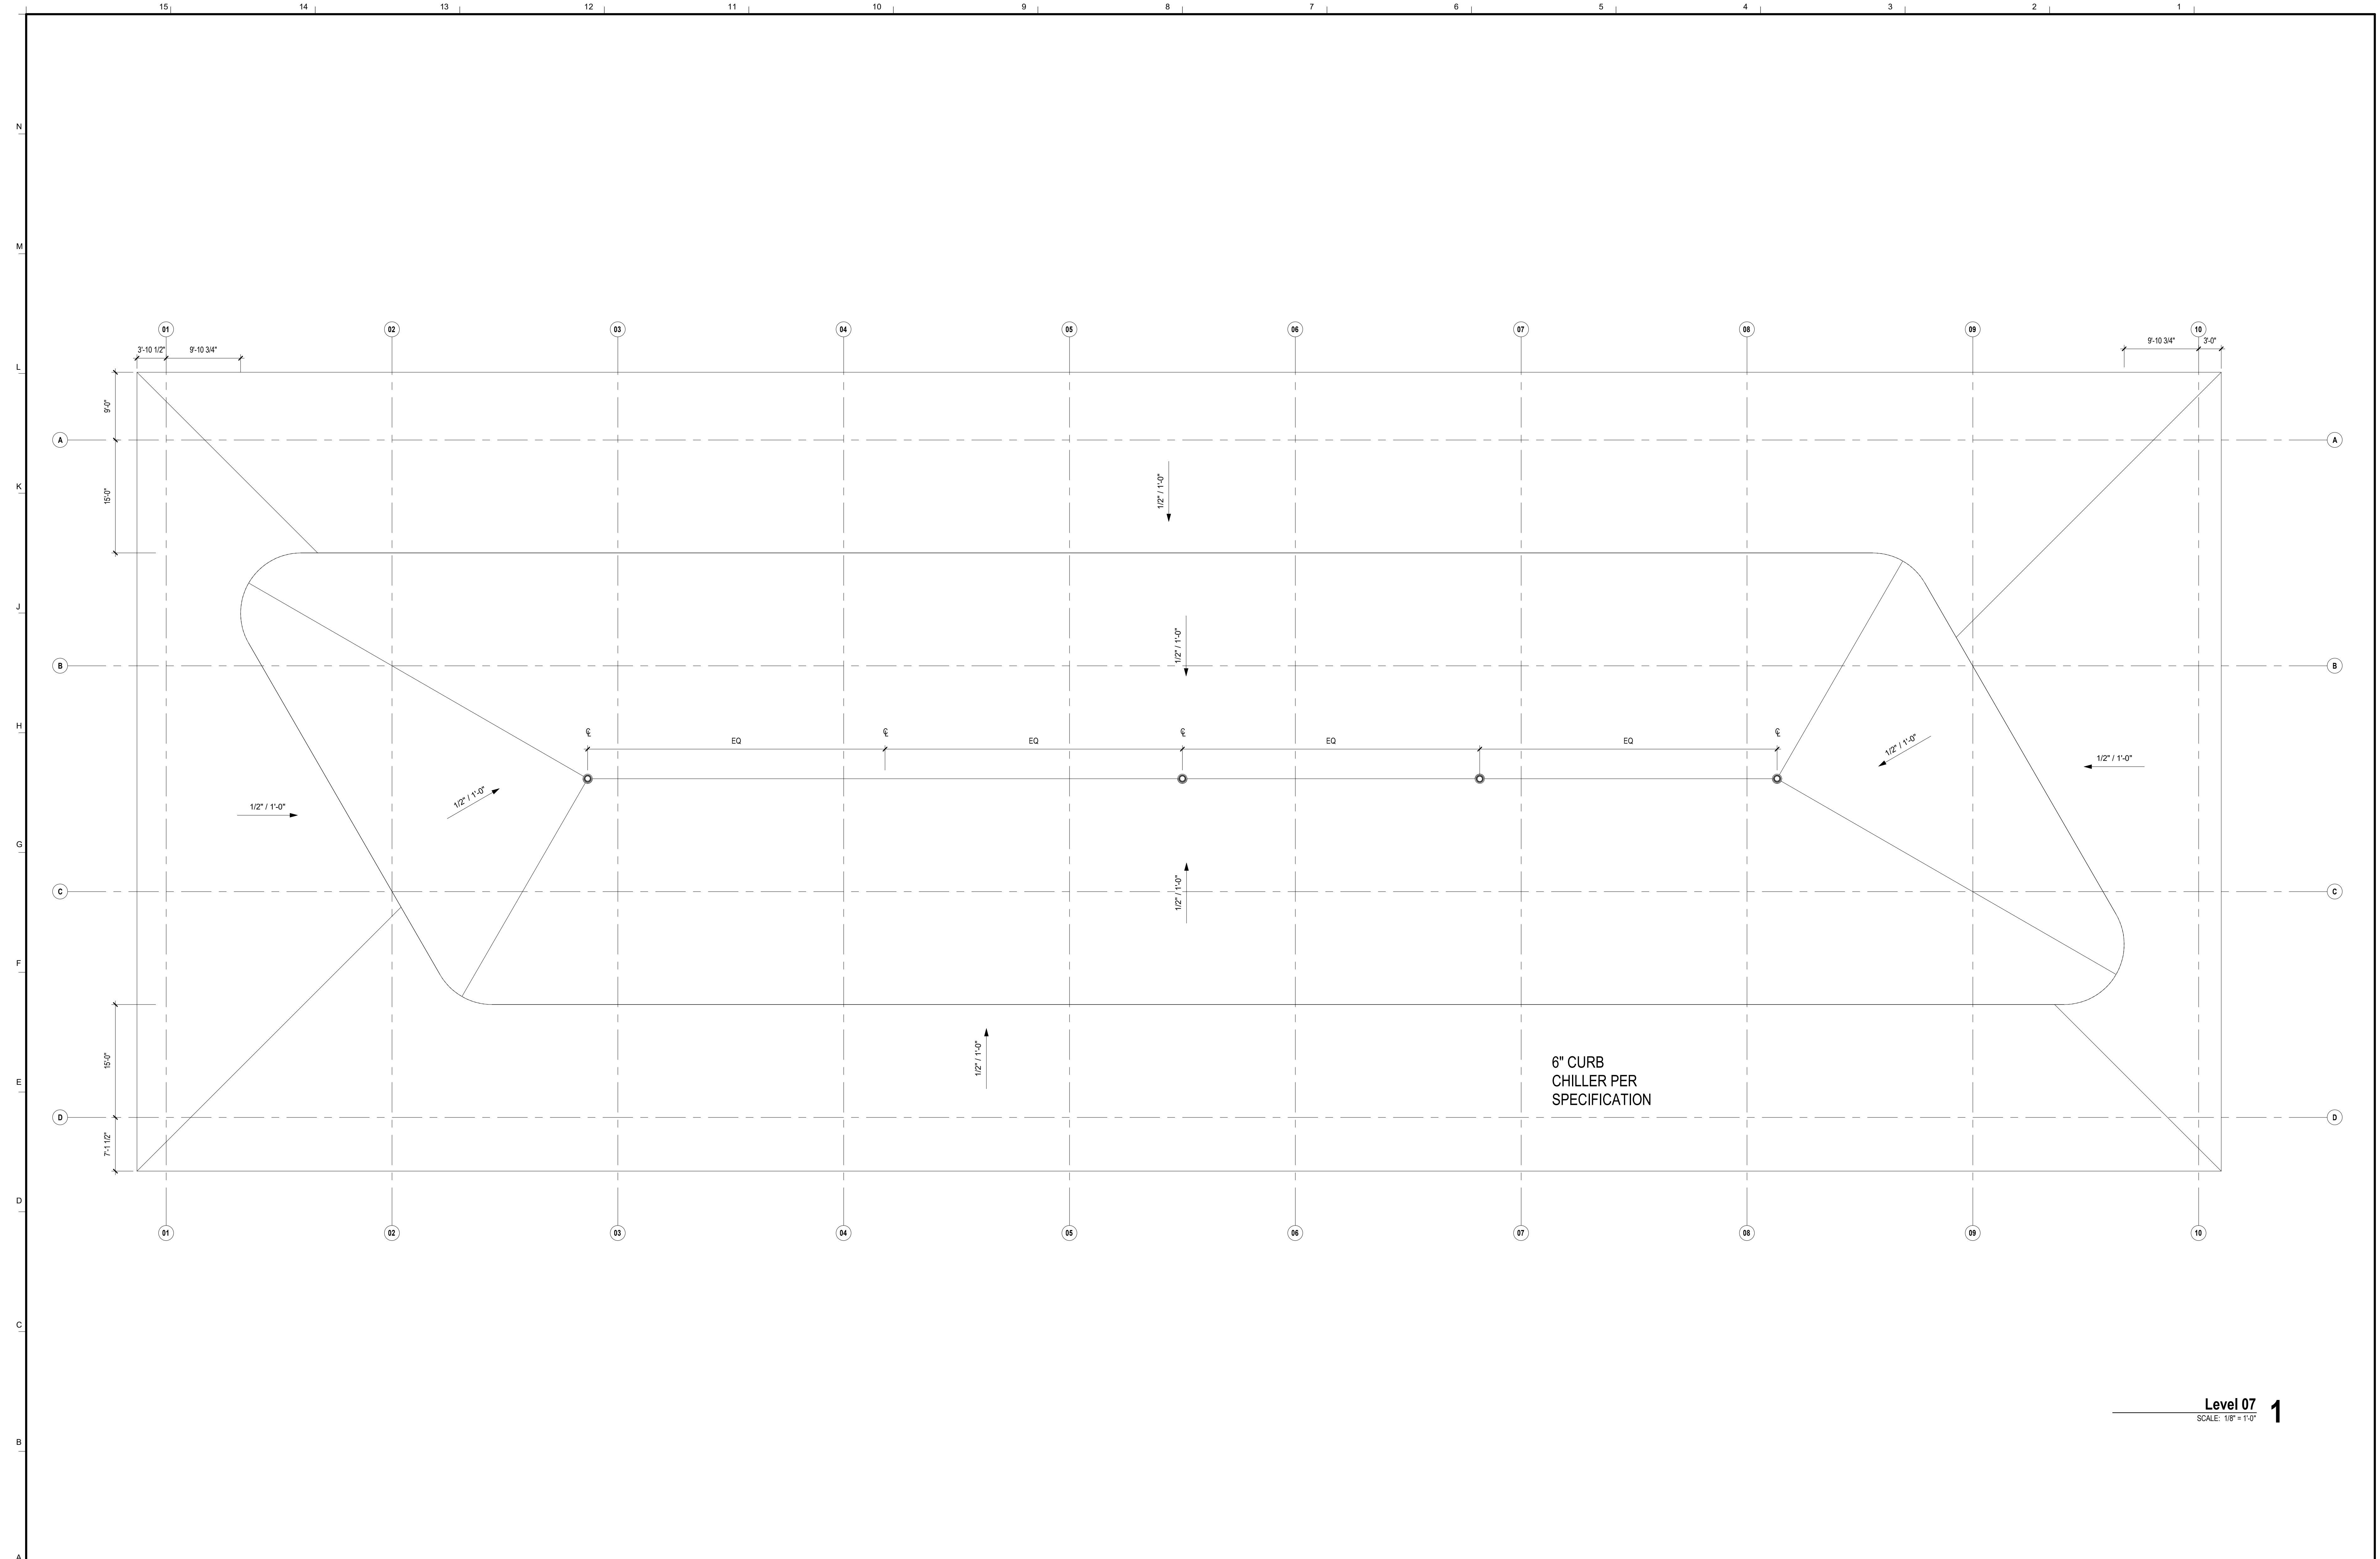

BLUEBEAM

A NEMETSCHEK COMPANY

CAPTURE ENGINE

Mechanical Electrical Plumbing

1234 Miller St.
Manchester, NH 0693

RS | REVU ARCHITEC

5555 N. Broad St
Pasadena CA 9110

OFFICE BUILDING

Project No: 32323

THIS DRAWING IS INTENDED FOR
DEMONSTRATION PURPOSES
ONLY. DO NOT USE THIS
DRAWING FOR ANY OTHER
PURPOSE WITHOUT THE
EXPRESS WRITTEN PERMISSION
OF BLUEBEAM, INC.

DRAWING FOR ANY OTHER
PURPOSE WITHOUT THE
EXPRESS WRITTEN PERMISSION
OF BLUEBEAM, INC.

DATE	03	
ISSUED FOR:	INTERNAL	
PROJECT		
DRAWN BY:		
CHECKED BY:		
APPROVED BY:		
#	DATE	DESCRIP

DRAWN BY:
CHECKED BY:
APPROVED BY:

A large, bold, black sans-serif font is used for the text. The top line reads "NOT FOR CONSTRUCTION" in all caps, with "NOT FOR" on one line and "CONSTRUCTION" on the next. Below it, another line of all-caps text reads "CONFIDENTIAL". To the left of the main text block, there is a vertical column of smaller, black, all-caps text: "3232" at the top, followed by "Author", "Checker", "Approver", and "ION" stacked vertically.

STAMP

STAM

P:	SHEET TITLE & NUMBER ROOF PLAN
----	-----------------------------------

A2.6

15 | 14 | 13 | 12 | 11 | 10 | 9 | 8 | 7 | 6 | 5 | 4 | 3 | 2 | 1 |

M


L

K

J

H

G

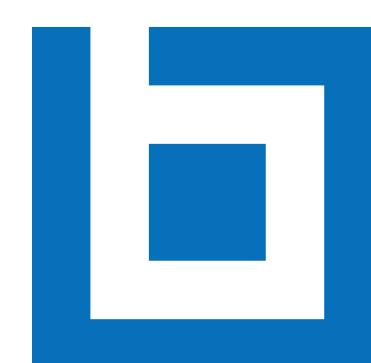

BLUEBEAM®

A NEMETSCHEK COMPANY

CAPTURE ENGINE

Mechanical Electrical Plumbing

1234 Miller St.
Manchester, NH 0693

RS | REVU ARCHITE

5555 N. Broad St
Pasadena CA 9110

OFFICE BUILDING

Project No: 32323

THIS DRAWING IS INTENDED FOR
DEMONSTRATION PURPOSES
ONLY. DO NOT USE THIS
DRAWING FOR ANY OTHER
PURPOSE WITHOUT THE
EXPRESS WRITTEN PERMISSION
OF BLUEBEAM, INC.

DATE	03/04/20	
ISSUED FOR:	INTERNAL REVIEW	
PROJECT	32	
DRAWN BY:	Aut	
CHECKED BY:	Chec	
APPROVED BY:	Appro	
#	DATE	DESCRIPTION

NOT FOR CONSTRUCTION

CONFIDENTIAL


STAM

10 of 10

STAMP:

SHEET TITLE & NUMBER

A6.02

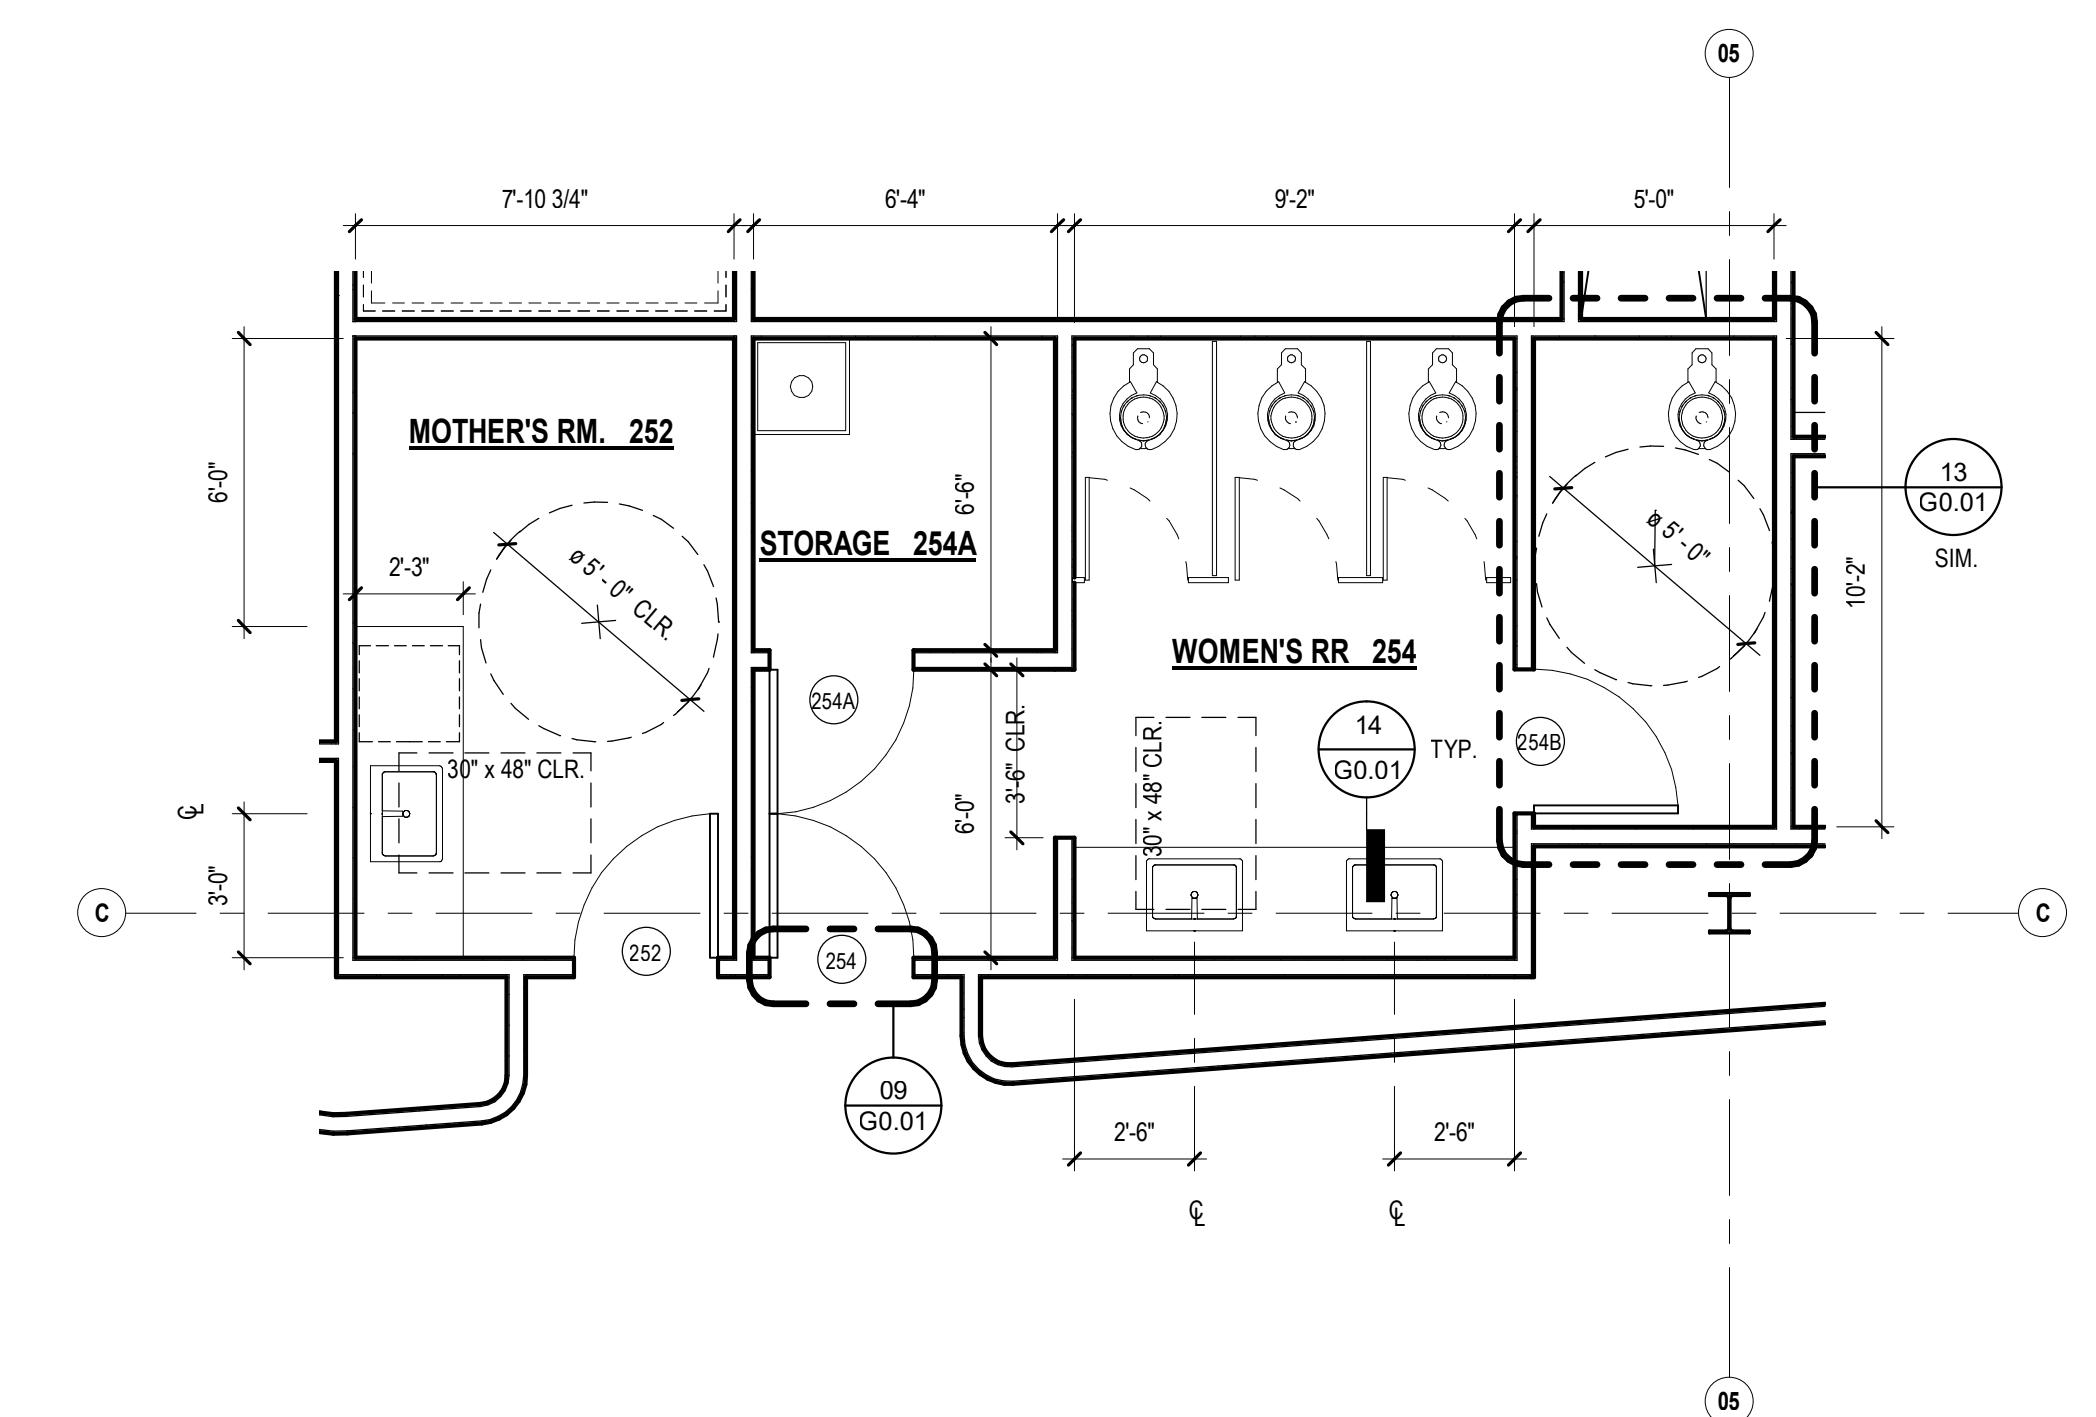


Level 02 - Callout 1

SCALE: 1/4" = 1'-0"

© 2018 Bluebeam, Inc.

15 | 14 | 13 | 12 | 11 | 10 | 9 | 8 | 7 | 6 | 5 | 4 | 3 | 2 | 1 |

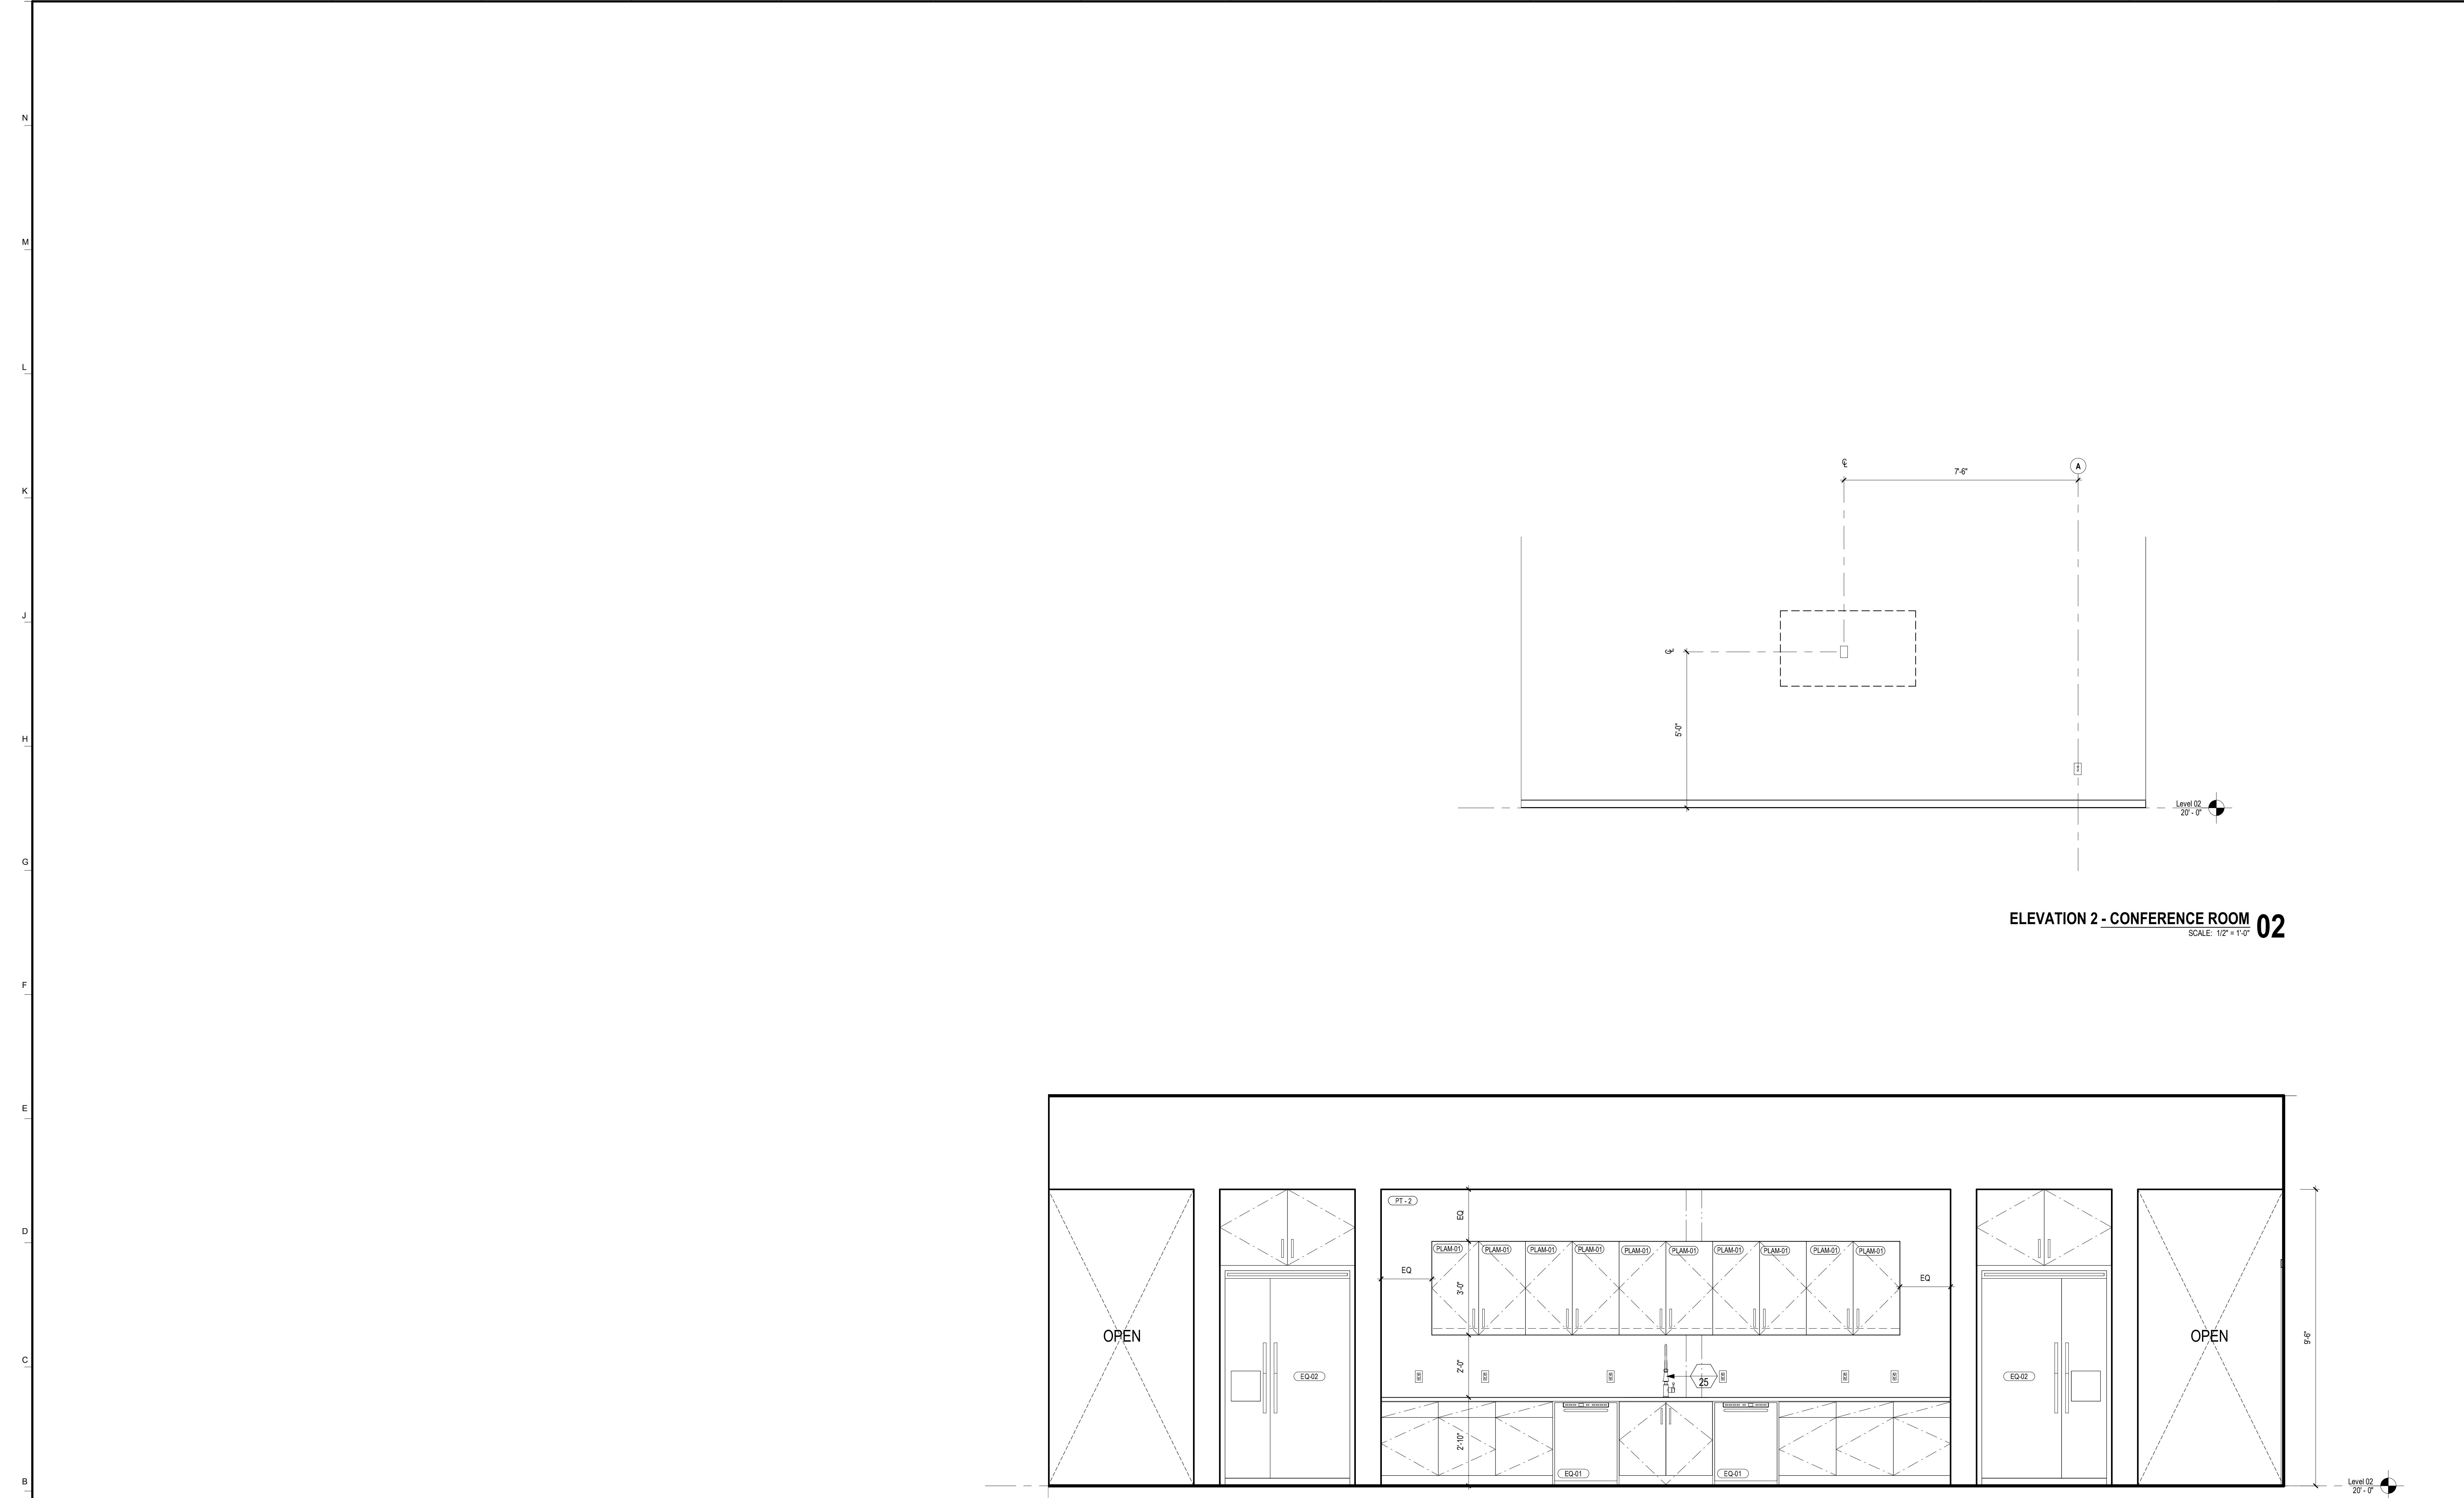


ELEVATION 2 - CONFERENCE ROOM 02

SCALE: 1/2" = 1'-0"

ELEVATION 1 - BREAK ROOM 233 01

SCALE: 1/2" = 1'-0"

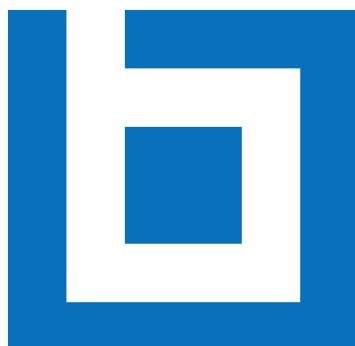 BLUEBEAM® A NEMETSCHEK COMPANY	CAPTURE ENGINEERS Mechanical Electrical Plumbing 1234 Miller St. Manchester, NH 06930	REVU ARCHITECTS 5555 N. Broad St Pasadena CA 91101	OFFICE BUILDING Project No: 323232 Project Address: 123 Schonsett St Chicago, IL 60601	THIS DRAWING IS INTENDED FOR DEMONSTRATION PURPOSES ONLY. DO NOT USE THIS DRAWING FOR ANY OTHER PURPOSE WITHOUT THE EXPRESS WRITTEN PERMISSION OF BLUEBEAM, INC.	DATE ISSUED FOR: 03/04/2019 INTERNAL REVIEW PROJECT: 3232 DRAWN BY: Author CHECKED BY: Checker APPROVED BY: Approver <table border="1"><tr><td>#</td><td>DATE</td><td>DESCRIPTION</td></tr></table>	#	DATE	DESCRIPTION	NOT FOR CONSTRUCTION CONFIDENTIAL	STAMP:	STAMP:	SHEET TITLE & NUMBER INTERIOR ELEVATIONS A7.01
#	DATE	DESCRIPTION										

DOOR SCHEDULE

OPENING			RATING	OPENING SIZE		DOOR		GLASS TYPE	FRAME			REMARKS
ROOM NUMBER	TAG	RM NAME		WIDTH	HEIGHT	MATERIAL	FINISH		TYPE	MATERIAL	FINISH	
201	201	MEETING	NR	3'-0"	7'-0"	HM	P1A	NA	HM	PAINT P3	SA	
202	202	MEETING	NR	3'-0"	7'-0"	HM	P1A	NA	HM	PAINT P3	SA	
203			NR	3'-0"	7'-0"	HM	P1A	NA	HM	PAINT P3	SA	
204			NR	3'-0"	7'-0"	HM	P1A	NA	HM	PAINT P3	SA	
205			NR	3'-0"	7'-0"	HM	P1A	NA	HM	PAINT P3	SA	
206			NR	3'-0"	7'-0"	HM	P1A	NA	HM	PAINT P3	SA	
207	207A	CONFERENCE	NR	2'-10"	6'-8"	WD	P3	GL2	WD	PAINT P2	2B	
207	207B	CONFERENCE	NR	2'-10"	6'-8"	WD	P3	GL2	WD	PAINT P2	2B	
208	208	MEETING	NR	2'-10"	6'-8"	WD	P3	GL2	WD	PAINT P2	2B	
209	209	RECEPTION	NR	2'-10"	6'-8"	WD	P3	GL2	WD	PAINT P2	2B	
210	210	MEETING	NR	2'-10"	6'-8"	WD	P3	GL2	WD	PAINT P2	2B	
211	211A	CONFERENCE	NR	2'-10"	6'-8"	WD	P3	GL2	WD	PAINT P2	2B	
211	211B	CONFERENCE	NR	2'-10"	6'-8"	WD	P3	GL2	WD	PAINT P2	2B	
212	212	OFFICE	NR	3'-0"	7'-0"	HM	P1A	NA	HM	PAINT P3	SA	
213	213	OFFICE	NR	3'-0"	7'-0"	HM	P1A	NA	HM	PAINT P3	SA	
214	214	MEETING	NR	3'-0"	7'-0"	HM	P1A	NA	HM	PAINT P3	SA	
215	215	MEETING	NR	3'-0"	7'-0"	HM	P1A	NA	HM	PAINT P3	SA	
216	216	OPEN OFFICE	NR	3'-0"	7'-0"	HM	P1A	NA	HM	PAINT P3	SA	
217	217	OPEN OFFICE	NR	3'-0"	7'-0"	HM	P1A	NA	HM	PAINT P3	SA	
223			NR	3'-0"	7'-0"	HM	P1A	NA	HM	PAINT P3	SA	
224			NR	3'-0"	7'-0"	HM	P1A	NA	HM	PAINT P3	SA	
225			NR	3'-0"	7'-0"	HM	P1A	NA	HM	PAINT P3	SA	
226			NR	3'-0"	7'-0"	HM	P1A	NA	HM	PAINT P3	SA	
227	227	OFFICE	NR	3'-0"	7'-0"	HM	P1A	NA	HM	PAINT P3	SA	
228			NR	3'-0"	7'-0"	HM	P1A	NA	HM	PAINT P3	SA	
229			NR	3'-0"	7'-0"	HM	P1A	NA	HM	PAINT P3	SA	
230			NR	3'-0"	7'-0"	HM	P1A	NA	HM	PAINT P3	SA	
231	231	BREAK	NR	3'-0"	7'-0"	HM	P1A	NA	HM	PAINT P3	SA	
232			NR	3'-0"	7'-0"	HM	P1A	NA	HM	PAINT P3	SA	
234			NR	3'-0"	7'-0"	HM	P1A	NA	HM	PAINT P3	SA	
235	235	MEETING	NR	3'-0"	7'-0"	HM	P1A	NA	HM	PAINT P3	SA	
236	236	OFFICE	NR	3'-0"	7'-0"	HM	P1A	NA	HM	PAINT P3	SA	
237	237	OFFICE	NR	3'-0"	7'-0"	HM	P1A	NA	HM	PAINT P3	SA	
238			NR	3'-0"	7'-0"	HM	P1A	NA	HM	PAINT P3	SA	
239	239	OFFICE	NR	3'-0"	7'-0"	HM	P1A	NA	HM	PAINT P3	SA	
240	240	OFFICE	NR	3'-0"	7'-0"	HM	P1A	NA	HM	PAINT P3	SA	
241	241	OFFICE	NR	3'-0"	7'-0"	HM	P1A	NA	HM	PAINT P3	SA	
242	242	OFFICE	NR	3'-0"	7'-0"	HM	P1A	NA	HM	PAINT P3	SA	
243	243	OFFICE	NR	3'-0"	7'-0"	HM	P1A	NA	HM	PAINT P3	SA	
245	245	MEETING	NR	2'-10"	6'-8"	WD	P3	GL2	WD	PAINT P2	2B	
246	246A	CONFERENCE	NR	2'-10"	6'-8"	WD	P3	GL2	WD	PAINT P2	2B	
246	246B	CONFERENCE	NR	2'-10"	6'-8"	WD	P3	GL2	WD	PAINT P2	2B	
247	247	MEETING	NR	2'-10"	6'-8"	WD	P3	GL2	WD	PAINT P2	2B	
249	249	OFFICE	NR	3'-0"	7'-0"	HM	P1A	NA	HM	PAINT P3	SA	
250	250	COPY	NR	3'-0"	7'-0"	HM	P1A	NA	HM	PAINT P3	SA	
251	251	STAIR	NR	3'-0"	7'-0"	HM	P1A	NA	HM	PAINT P3	SA	
252			NR	3'-0"	7'-0"	HM	P1A	NA	HM	PAINT P3	SA	
253	253	RECEPTION	NR	3'-0"	7'-0"	HM	P1A	NA	HM	PAINT P3	SA	
253A	253A	STORAGE	NR	2'-10"	6'-8"	HM	P1A	NA	HM	PAINT P3	SA	
254	254	WOMENS RR	NR	3'-0"	7'-0"	HM	P1A	NA	HM	PAINT P3	SA	
254	254A	WOMENS RR	NR	3'-0"	7'-0"	HM	P1A	NA	HM	PAINT P3	SA	
254B			NR	3'-0"	7'-0"	HM	P1A	NA	HM	PAINT P3	SA	
257	257	SERVER	NR	3'-0"	7'-0"	HM	P1A	NA	HM	PAINT P3	SA	
258			NR	3'-0"	7'-0"	HM	P1A	NA	HM	PAINT P3	SA	
258A	258A	STORAGE	NR	3'-0"	7'-0"	HM	P1A	NA	HM	PAINT P3	SA	
258B	258B	MENS RR	NR	3'-0"	7'-0"	HM	P1A	NA	HM	PAINT P3	SA	
259	259	STAIR	NR	3'-0"	7'-0"	HM	P1A	NA	HM	PAINT P3	SA	
255	260	RECEPTION	NR	3'-0"	7'-0"	HM	P1A	NA	HM	PAINT P3	SA	
261	261	OPEN OFFICE	NR	3'-0"	7'-0"	HM	P1A	NA	HM	PAINT P3	SA	
262	262	OPEN OFFICE	NR	3'-0"	7'-0"	HM	P1A	NA	HM	PAINT P3	SA	
264			NR	2'-10"	6'-8"	WD	P3	GL2	WD	PAINT P2	2B	
265A			NR	2'-10"	6'-8"	WD	P3	GL2	WD	PAINT P2	2B	
265B			NR	2'-10"	6'-8"	WD	P3	GL2	WD	PAINT P2	2B	
266			NR	2'-10"	6'-8"	WD	P3	GL2	WD	PAINT P2	2B	

Level 02: 64


Grand total: 64

DOOR / WINDOW ABBREVIATIONS**DOOR HARDWARE NOTES**

ALUM = ALUMINUM	P = PAINT	BU-FOLD = PANIC HARDWARE
CL = CLOSET	PH = PAIR	PR = PRE-FINISHED
GL = GLASS	SCW = SOLID CORE WOOD	RW = REMOVABLE MULLION
HCM = HOLLOW CORE WOOD	SGC = SOLID CORE WOOD	RO = ROUGH OPENING
HM = HOLLOW METAL	STL = STEEL	RT = RETROFITED
CF = CLEAR FINISH	CSMT = CEMENT	TR = SERVICE
CP = COPPER	FACT = FACTORY	VDF = VERTICAL GRAIN DOUGLAS
FX = FIXED	FAC = FACTORY	HDG = HDG
HGD = HGD	MANUF = MANUFACTURED	WD = FIR
LG = LAMINATED GLASS	CLR.ANNOD = CLR.ANNOD	SS = WOOD
SS = STAIN	SECURE = SEAL	\$ = SECURITY PROVISIONS
CLR.ANNOD = CLR.ANNOD	APPLY	

1. THE GENERAL CONTRACTOR SHALL PROVIDE AND INSTALL REQUIRED BUCK ASSEMBLIES AS SHOWN ON ARCHITECTS DRAWINGS, U.N.O.
2. THE GENERAL CONTRACTOR SHALL PROVIDE AND INSTALL DOORS AS SPECIFIED ON ARCHITECTURAL DRAWINGS, U.N.O.
3. COORDINATE KEYING OF EXISTING DOORS WITH NEW DOORS ALIKE. ALL ENTRANCES/EXITS TO BE KEYED ALIKE UNLESS ALL PRIVATE OFFICES TO BE KEYED SEPARATELY UNLESS ALL SUPPORT ROOMS ARE TO BE KEYED ALIKE U.N.O. COORDINATE MASTER KEYING WITH TENANT, LANDLORD, AND ARCHITECT. KEYING TO BE REFLECTED ON DOOR AND HARDWARE SUBMITTAL.
4. ALL LOCKSETS SHALL BE CODED AND/OR KEYED IN ACCORDANCE WITH THE BUILDING REQUIREMENTS. CODES AND/OR KEYS SHALL BE PROVIDED BY THE TENANT PROPERLY TESTED AND/OR TAGGED. THE NUMBER OF MASTER AND PASS KEYS SHALL BE COORDINATED WITH BUILDING MANAGEMENT.
5. CONTRACTOR SHALL SUBMIT A DETAILED HARDWARE LIST WHICH INDICATES THE QUANTITIES, TYPES, MANUFACTURERS, CATALOG NUMBERS AND LOCATIONS OF THE VARIOUS ARTICLES OF HARDWARE REQUIRED. HARDWARE LIST SHALL BE SUBMITTED NO LATER THAN 3

15 | 14 | 13 | 12 | 11 | 10 | 9 | 8 | 7 | 6 | 5 | 4 | 3 | 2 | 1 |

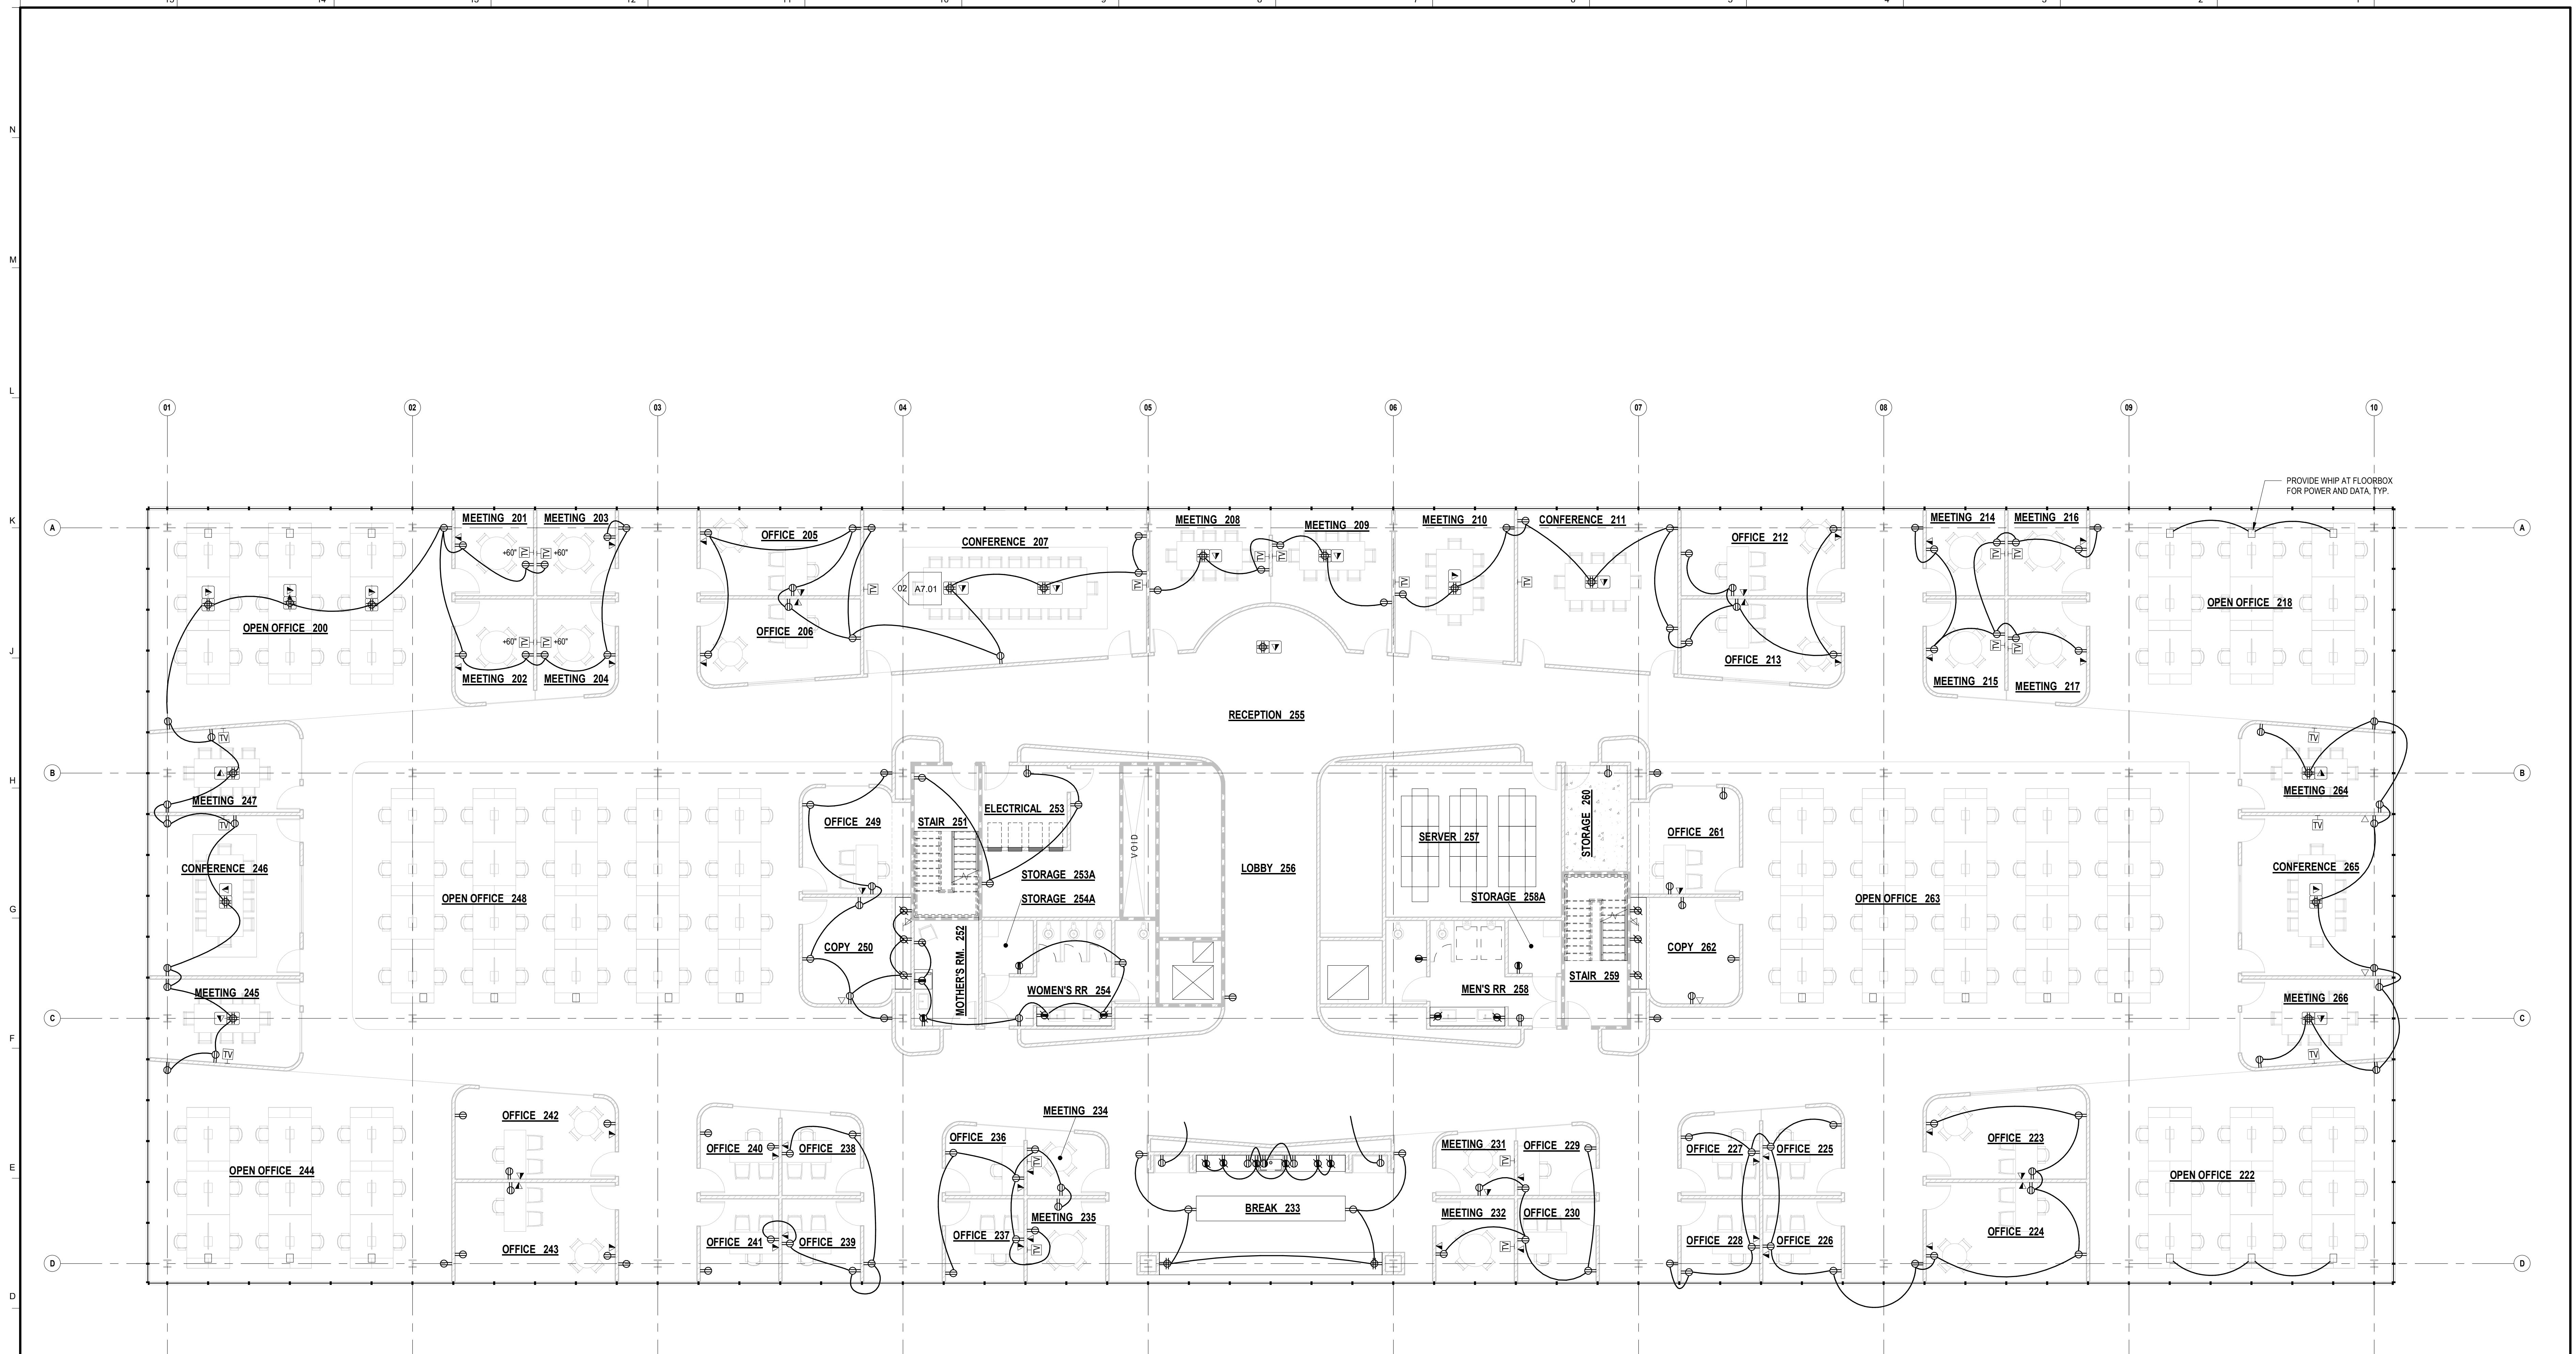

BLUEBEAM®
A NEMETSCHEK COMPANY

CAPTURE ENGINEERS
Mechanical
Electrical
Plumbing

1234 Miller St.
Manchester, NH 06930

REVU ARCHITECTS
5555 N. Broad St
Pasadena CA 91101

OFFICE BUILDING
Project No: 323232

Project Address:
123 Schonsett St
Chicago, IL 60601

THIS DRAWING IS INTENDED FOR
DEMONSTRATION PURPOSES
ONLY. DO NOT USE THIS
DRAWING FOR ANY OTHER
PURPOSE WITHOUT THE
EXPRESS WRITTEN PERMISSION
OF BLUEBEAM, INC.

DATE
ISSUED FOR: 03/04/2019
INTERNAL REVIEW


PROJECT: 3232
DRAWN BY: Author
CHECKED BY: Checker
APPROVED BY: Approver
DATE DESCRIPTION

**NOT FOR
CONSTRUCTION**
CONFIDENTIAL


STAMP:

STAMP:

SHEET TITLE & NUMBER
ELECTRICAL PLAN -
LEVEL 2
E2.02
© 2018 Bluebeam, Inc.

 


15 | 14 | 13 | 12 | 11 | 10 | 9 | 8 | 7 | 6 | 5 | 4 | 3 | 2 | 1 |

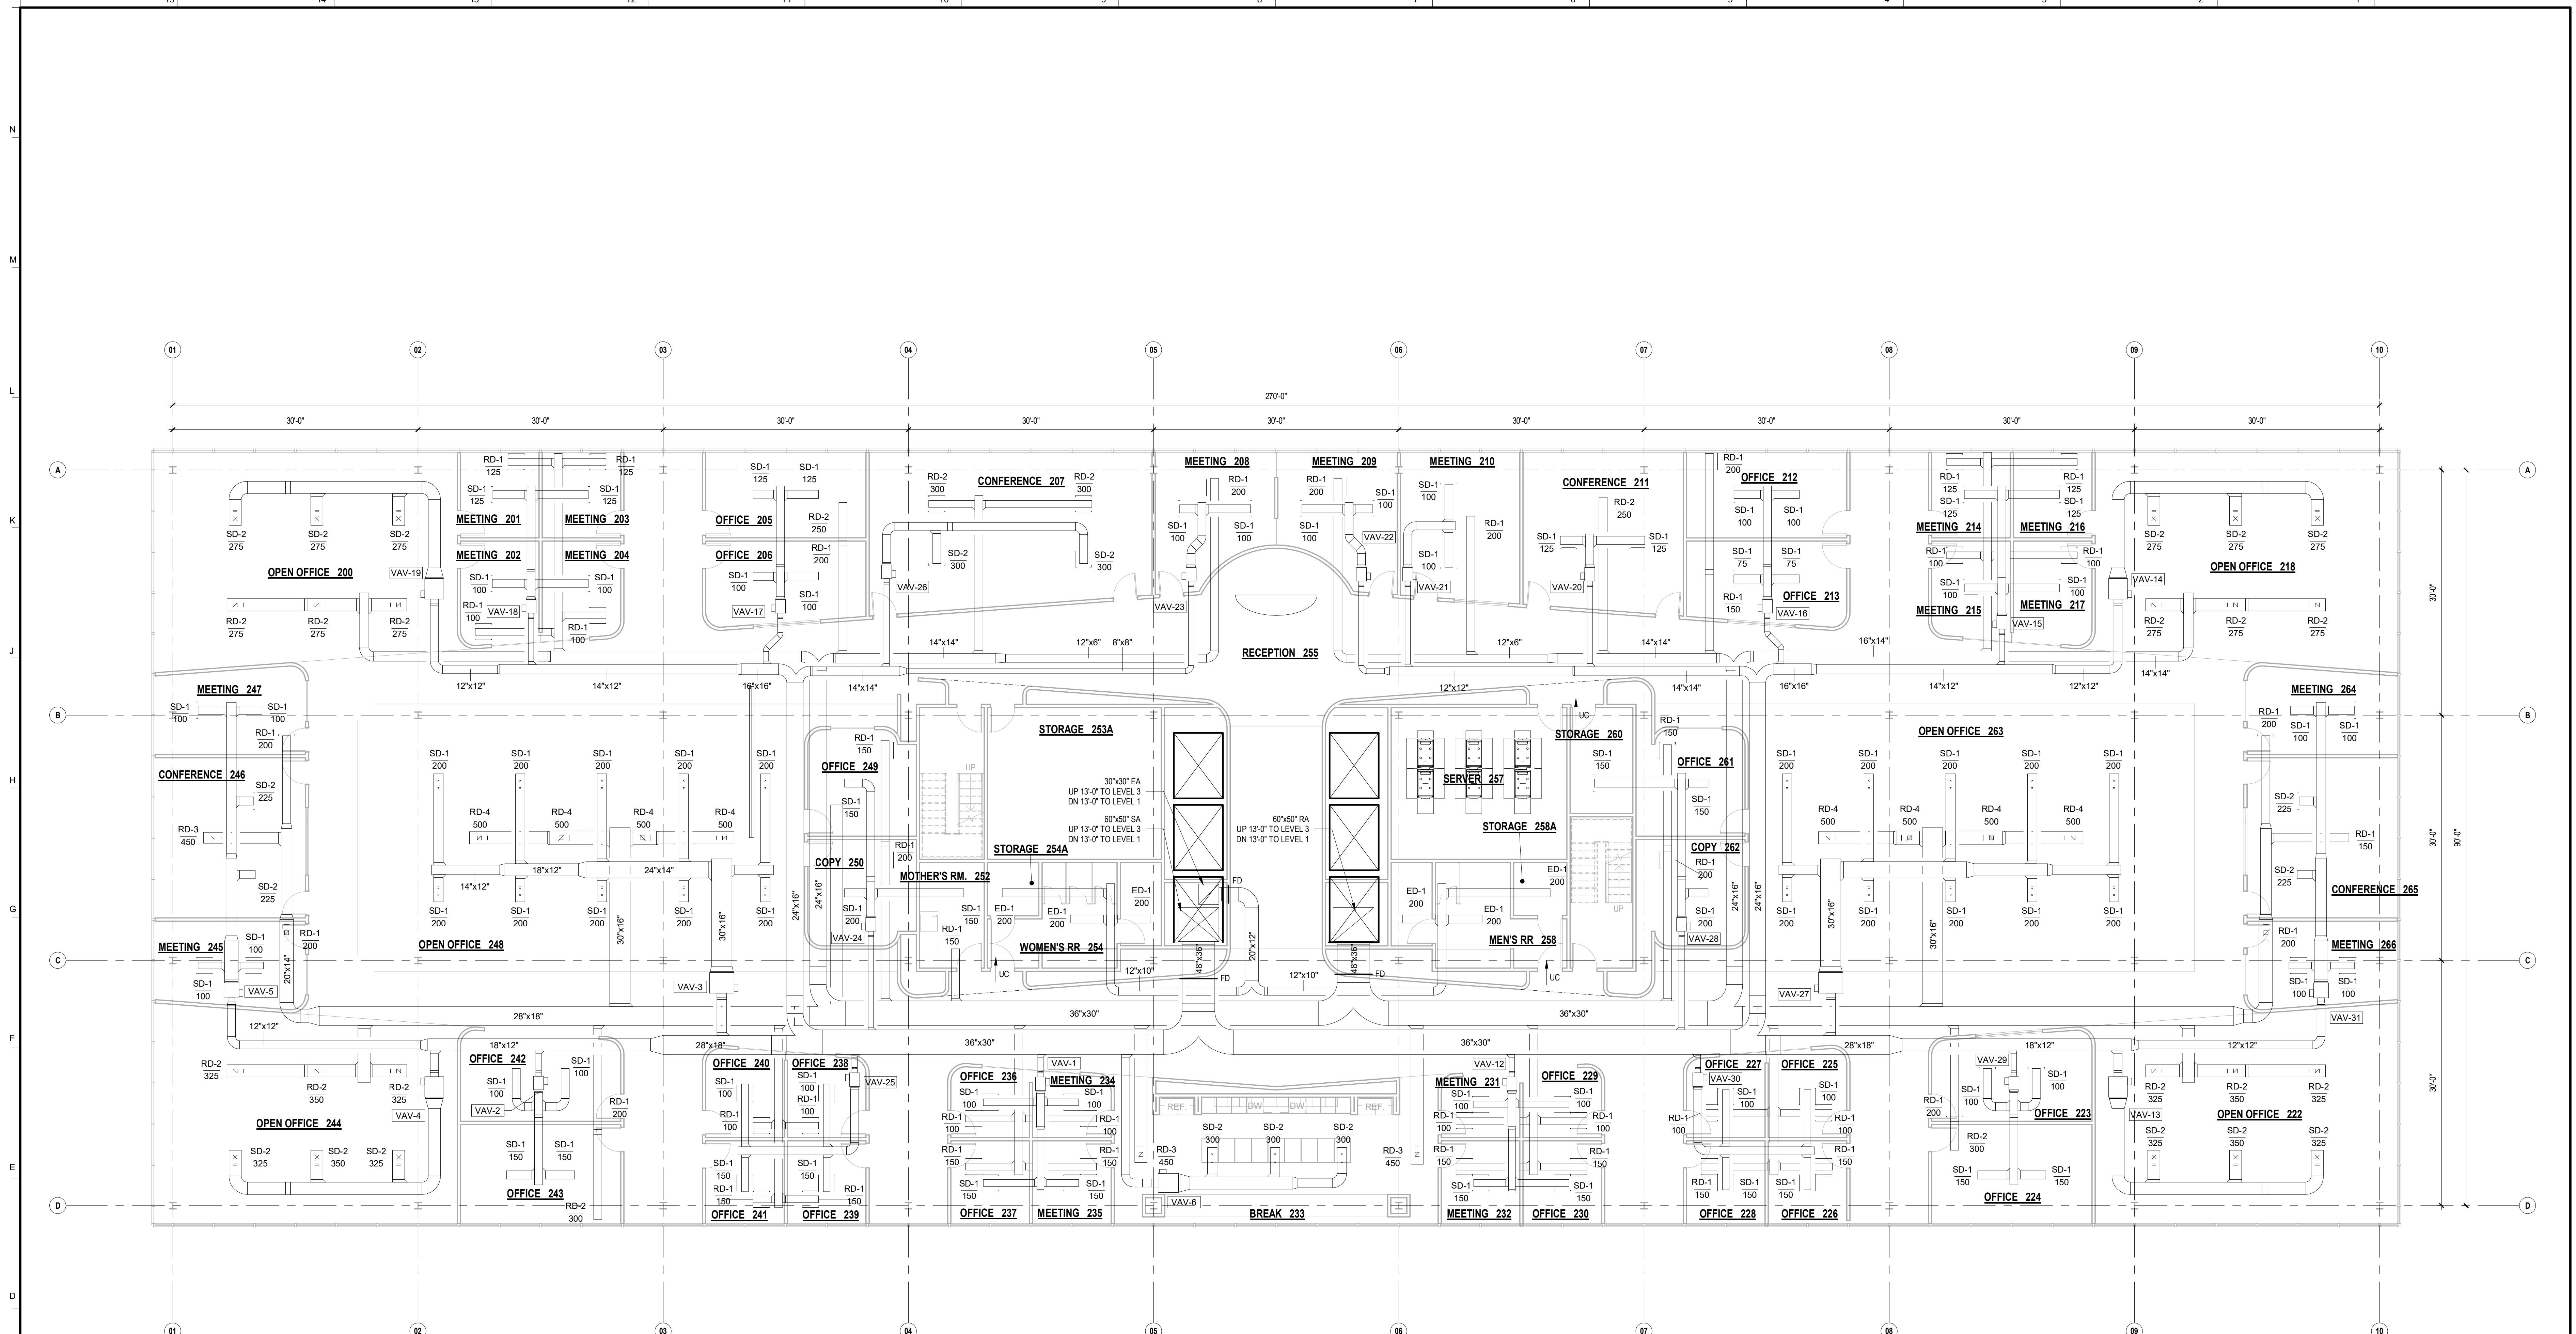

Level 02 HVAC 2
SCALE: 18"=1'-0"

15 | 14 | 13 | 12 | 11 | 10 | 9 | 8 | 7 | 6 | 5 | 4 | 3 | 2 | 1 |

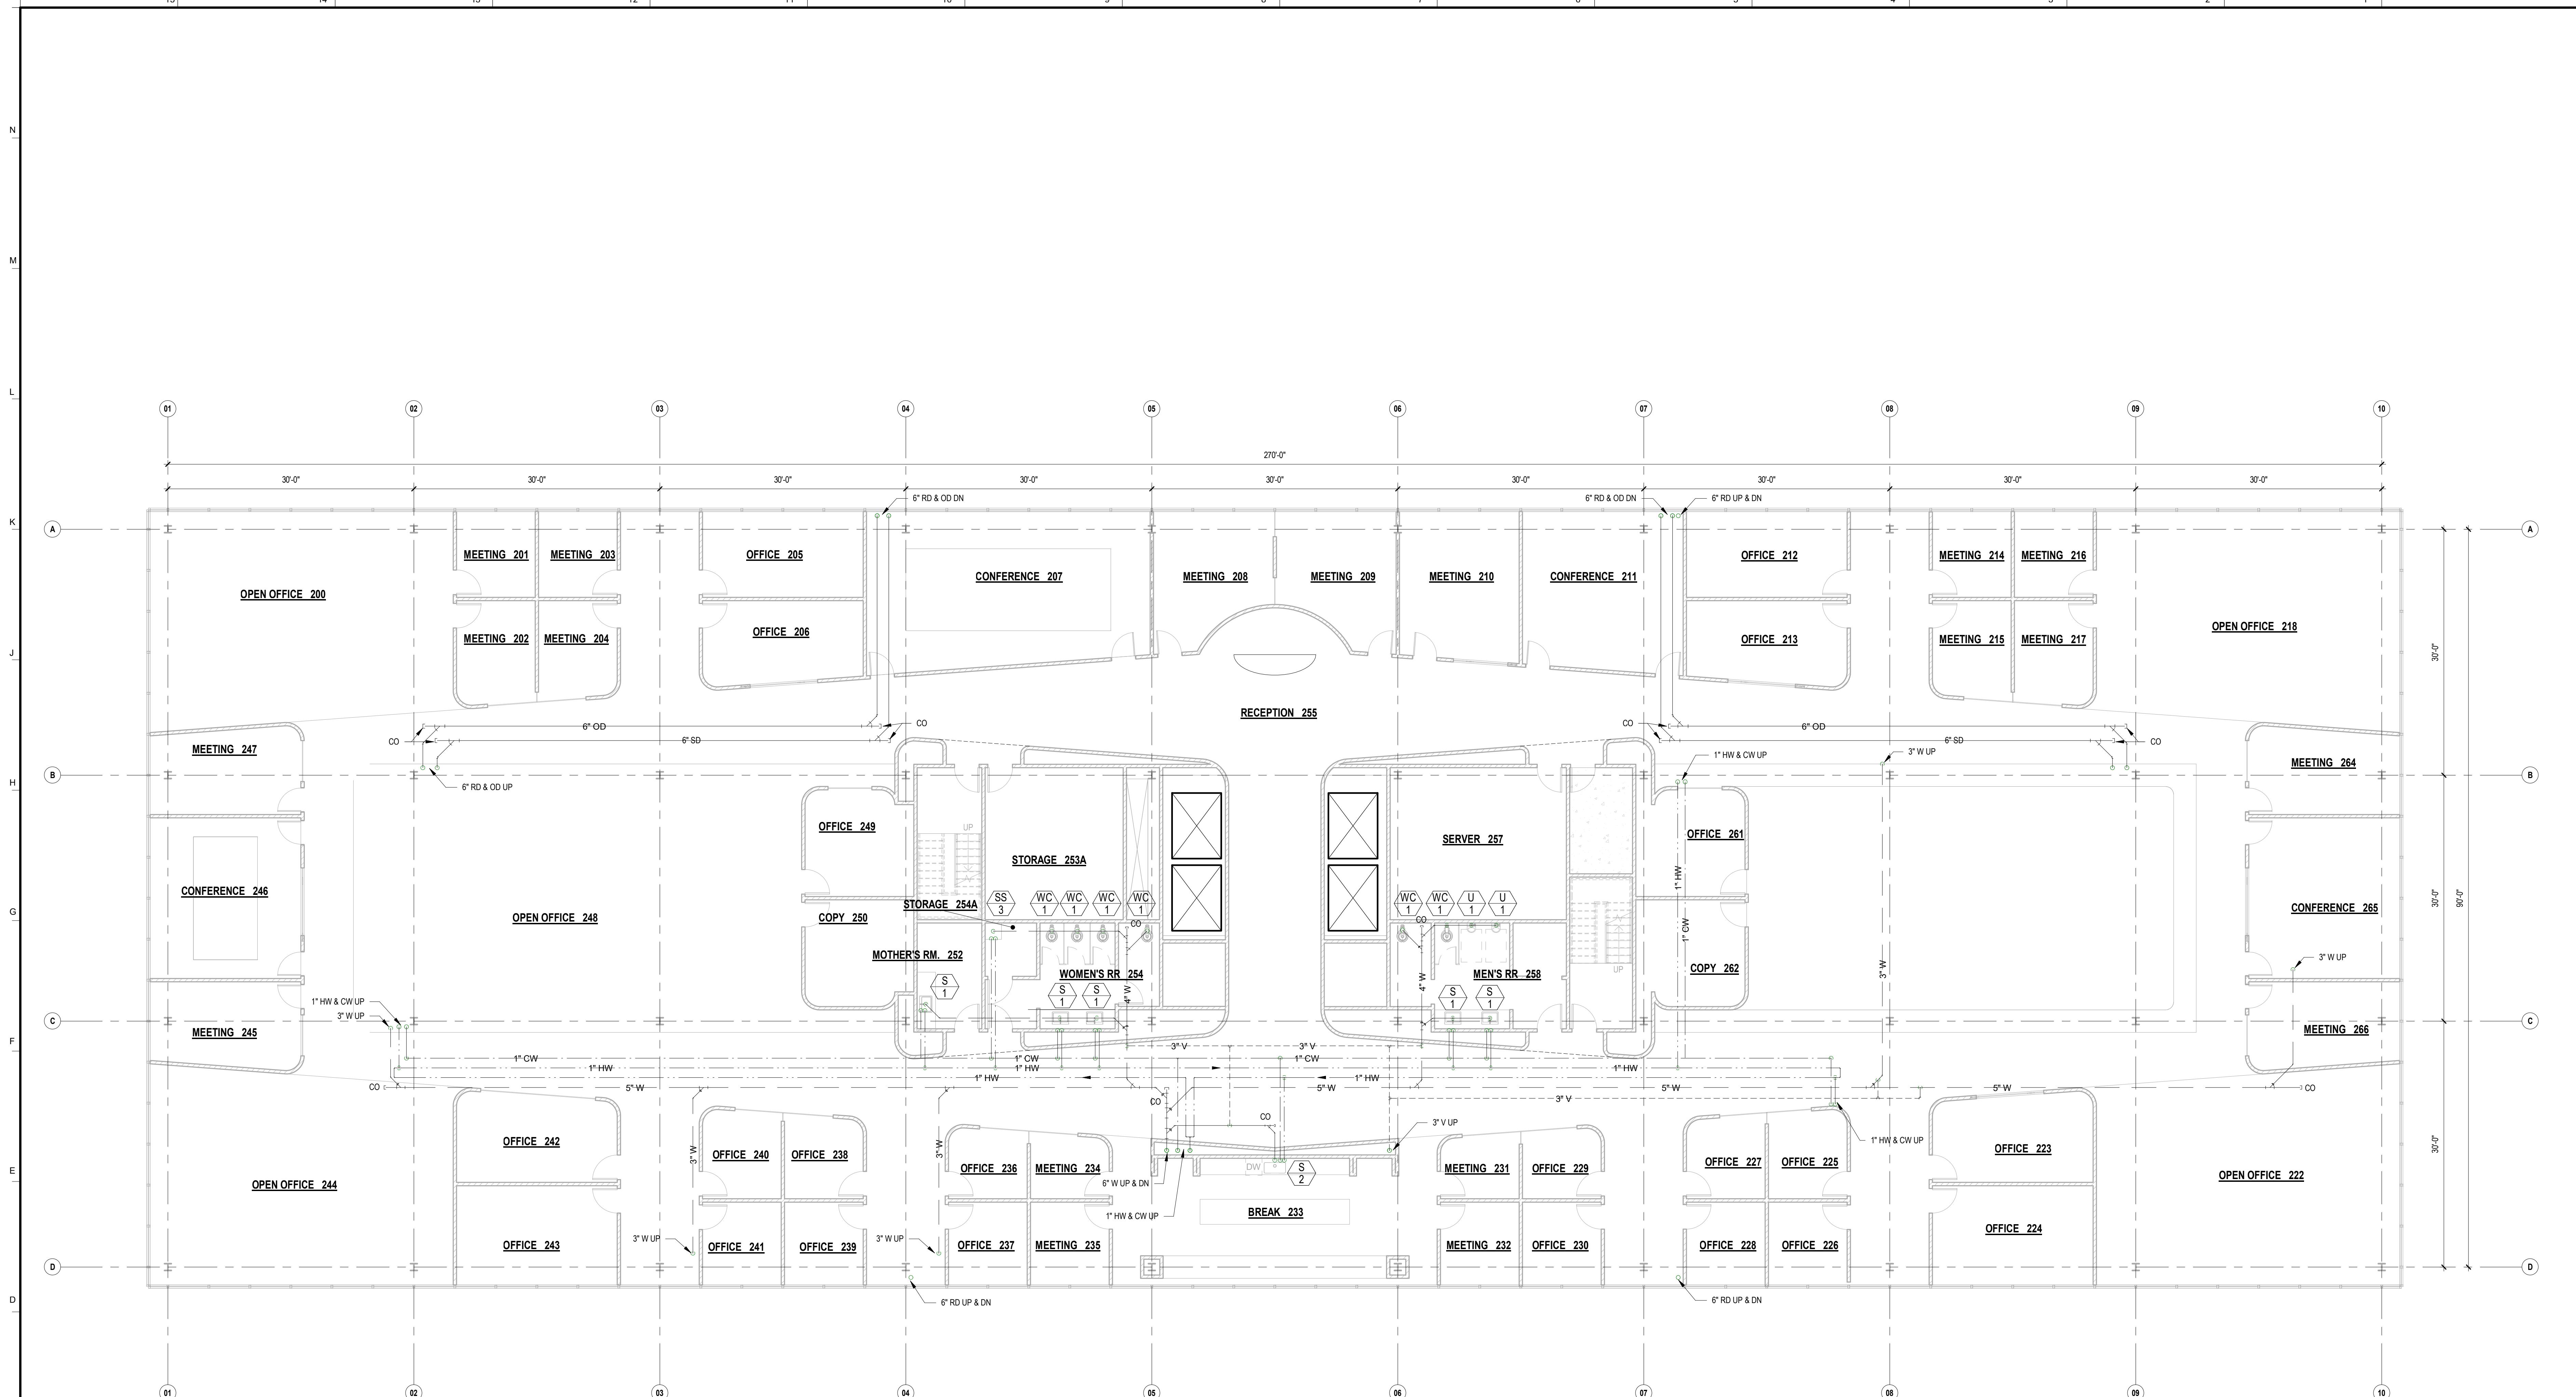

BLUEBEAM®
A NEMETSCHEK COMPANY

CAPTURE ENGINEERS
Mechanical
Electrical
Plumbing

1234 Miller St.
Manchester, NH 06930

REVU ARCHITECTS
5555 N. Broad St
Pasadena CA 91101

OFFICE BUILDING
Project No: 323232

Project Address:
123 Schonsett St
Chicago, IL 60601

THIS DRAWING IS INTENDED FOR
DEMONSTRATION PURPOSES
ONLY. DO NOT USE THIS
DRAWING FOR ANY OTHER
PURPOSE WITHOUT THE
EXPRESS WRITTEN PERMISSION
OF BLUEBEAM, INC.

DATE
ISSUED FOR: 03/04/2019
INTERNAL REVIEW

PROJECT: 3232
DRAWN BY: Author
CHECKED BY: Checker
APPROVED BY: Approver
| DATE | DESCRIPTION

**NOT FOR
CONSTRUCTION**
CONFIDENTIAL


STAMP:

STAMP:

SHEET TITLE & NUMBER
PLUMBING - LEVEL 2

P2.02

© 2018 Bluebeam, Inc.

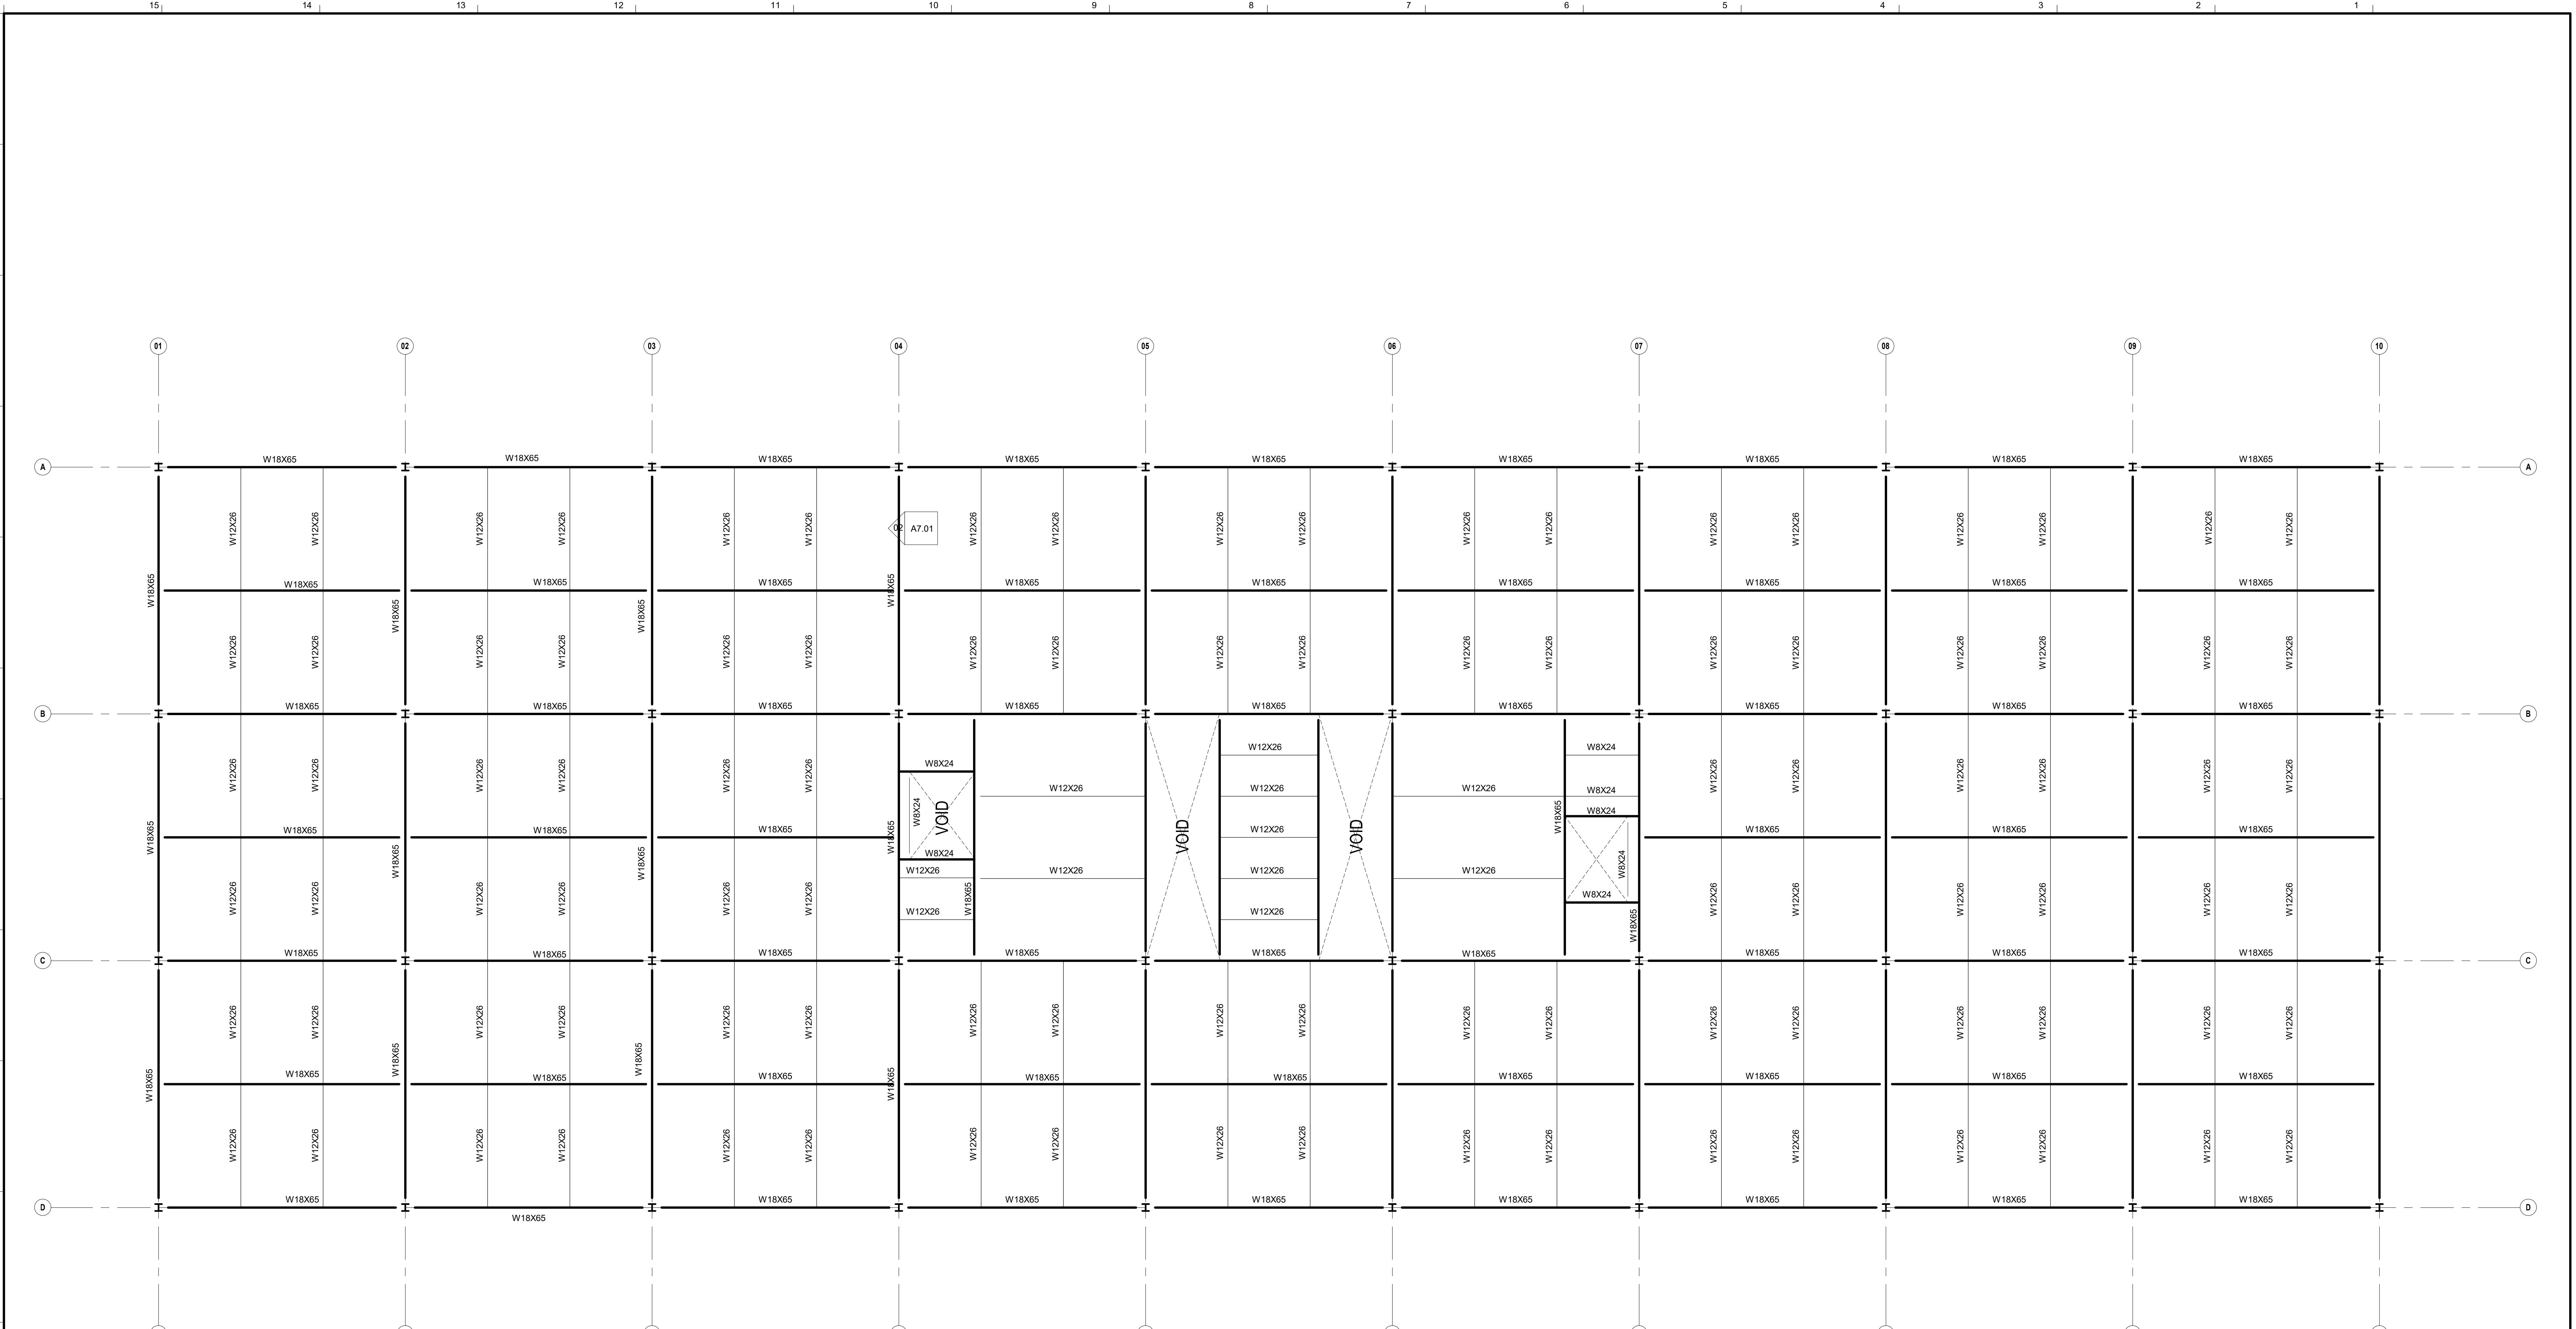

BLUEBEAM®
A NEMETSCHEK COMPANY

CAPTURE ENGINEERS
Mechanical
Electrical
Plumbing

1234 Miller St.
Manchester, NH 06930

REVU ARCHITECTS
5555 N. Broad St
Pasadena CA 91101

OFFICE BUILDING
Project No: 323232

Project Address:
123 Schonsett St
Chicago, IL 60601

THIS DRAWING IS INTENDED FOR
DEMONSTRATION PURPOSES
ONLY. DO NOT USE THIS
DRAWING FOR ANY OTHER
PURPOSE WITHOUT THE
EXPRESS WRITTEN PERMISSION
OF BLUEBEAM, INC.

DATE
ISSUED FOR: 03/04/2019
INTERNAL REVIEW

PROJECT: 3232
DRAWN BY: Author
CHECKED BY: Checker
APPROVED BY: Approver

#	DATE	DESCRIPTION
---	------	-------------

**NOT FOR
CONSTRUCTION**
CONFIDENTIAL

STAMP:

STAMP:

SHEET TITLE & NUMBER
LEVEL 02 FRAMING
PLAN
S2.02

© 2018 Bluebeam, Inc.